Interior Design Portfolio

Casen Carter

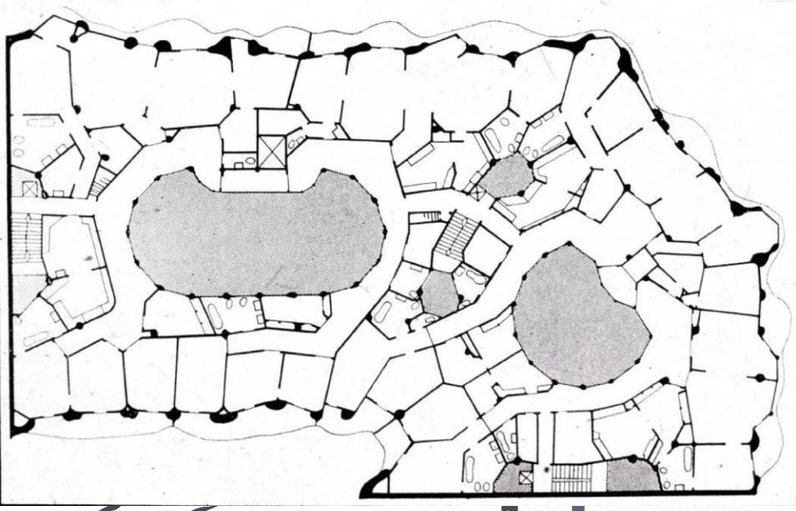

La Pedrera - Gaudi

Curvature and Flow

The design of this project revolves around the concept of curvature and flow. The goal is to connect space through organic shape. Connections allow users to collaborate and communicate easier within space. Organic shape creates unconventional and engaging design

Curvature and Flow

ID 4300 Commercial Design

Fall 2016

Main Office Building 2nd Floor

Main Office Building 1st Floor

Curvature and Flow

First Floor Café Section

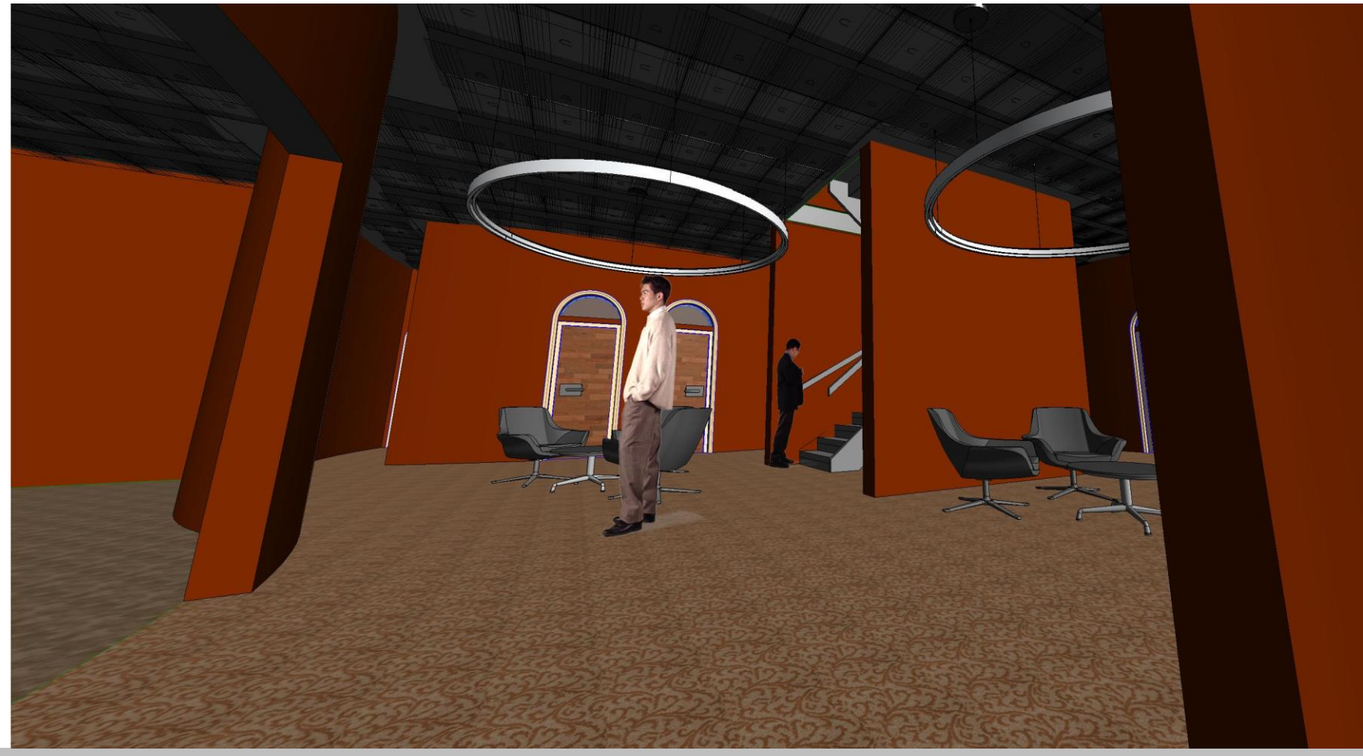

First Floor Lounge Perspective

Curvature and Flow

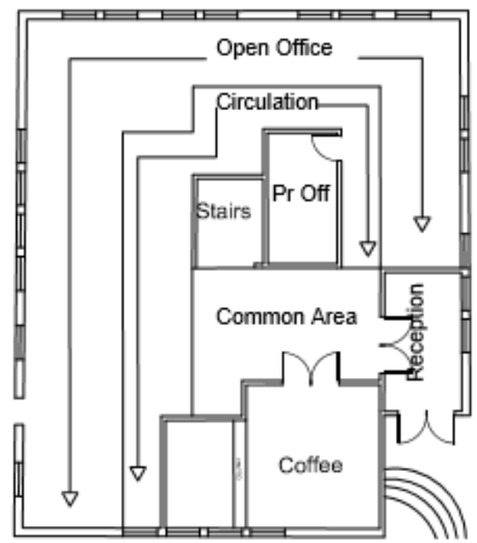

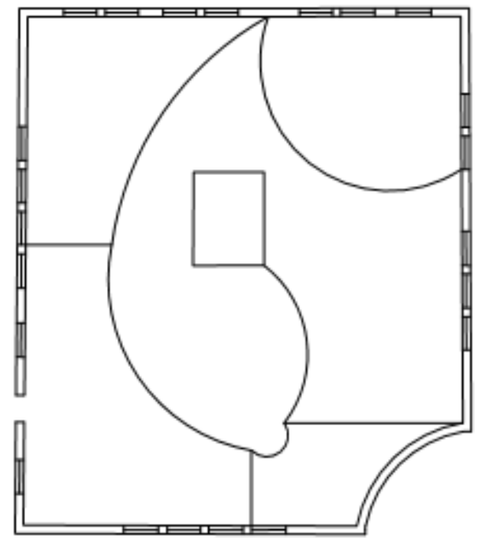

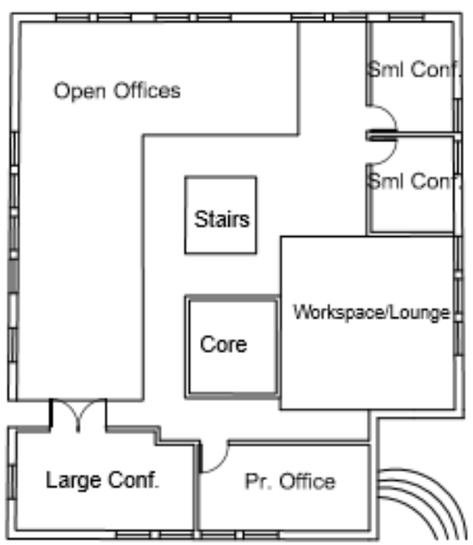

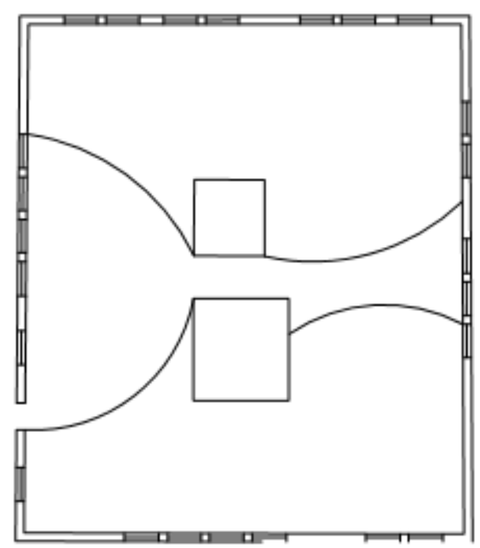

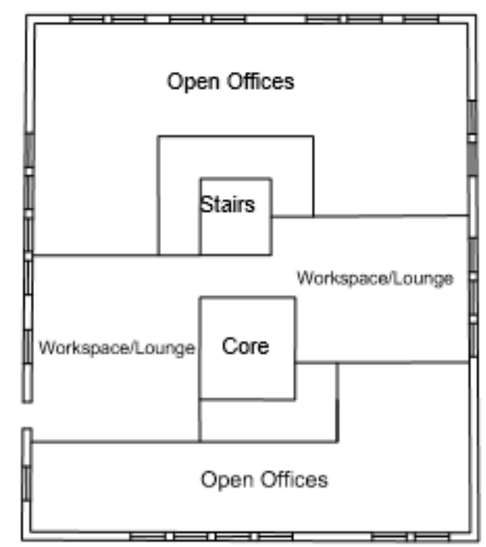

Process Documentation

Curvature and Flow

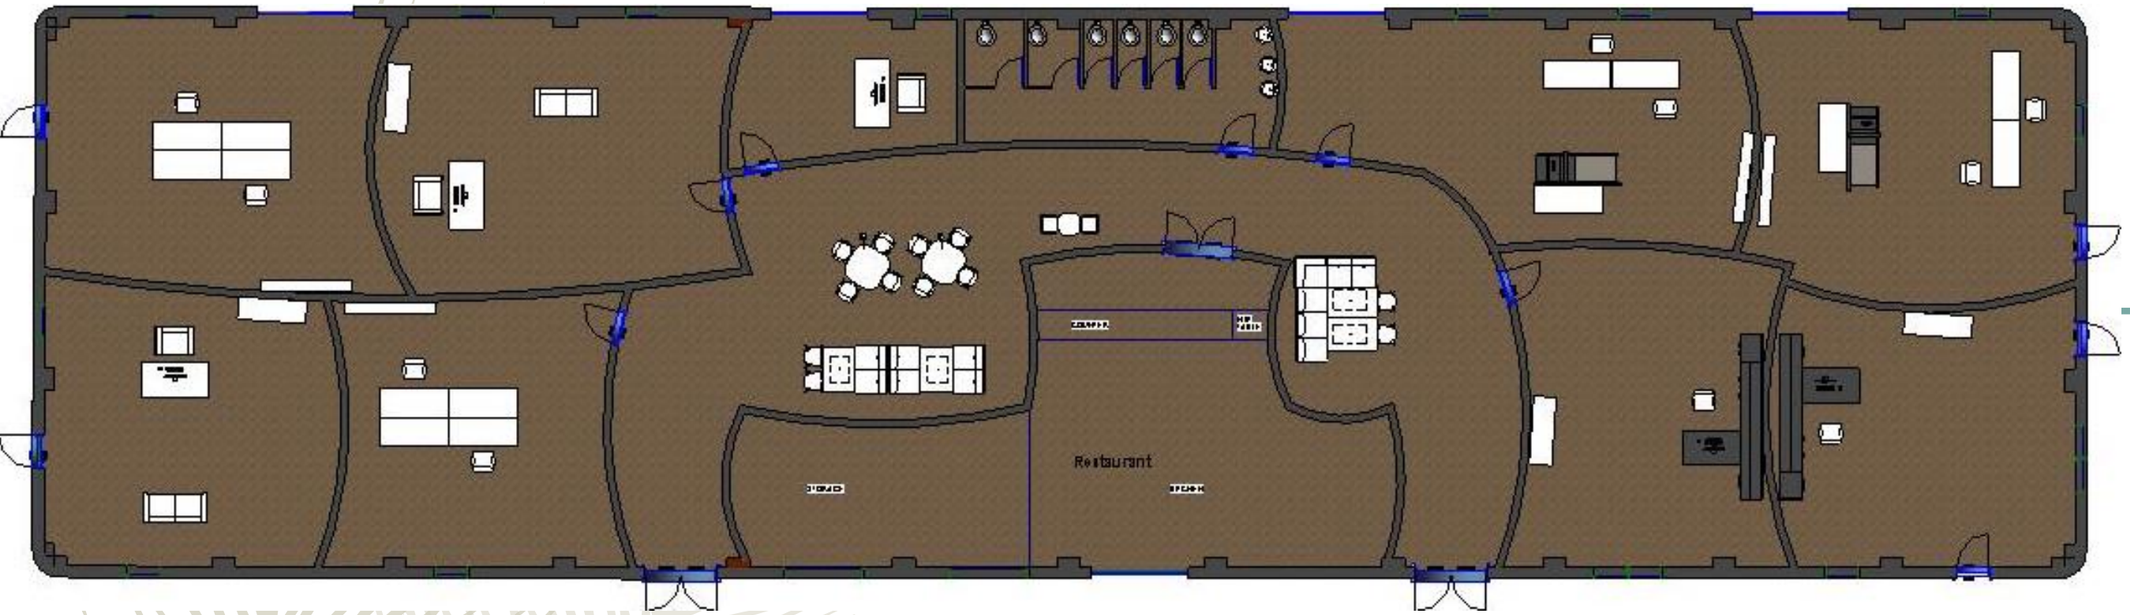

Building D (Artist Lofts)

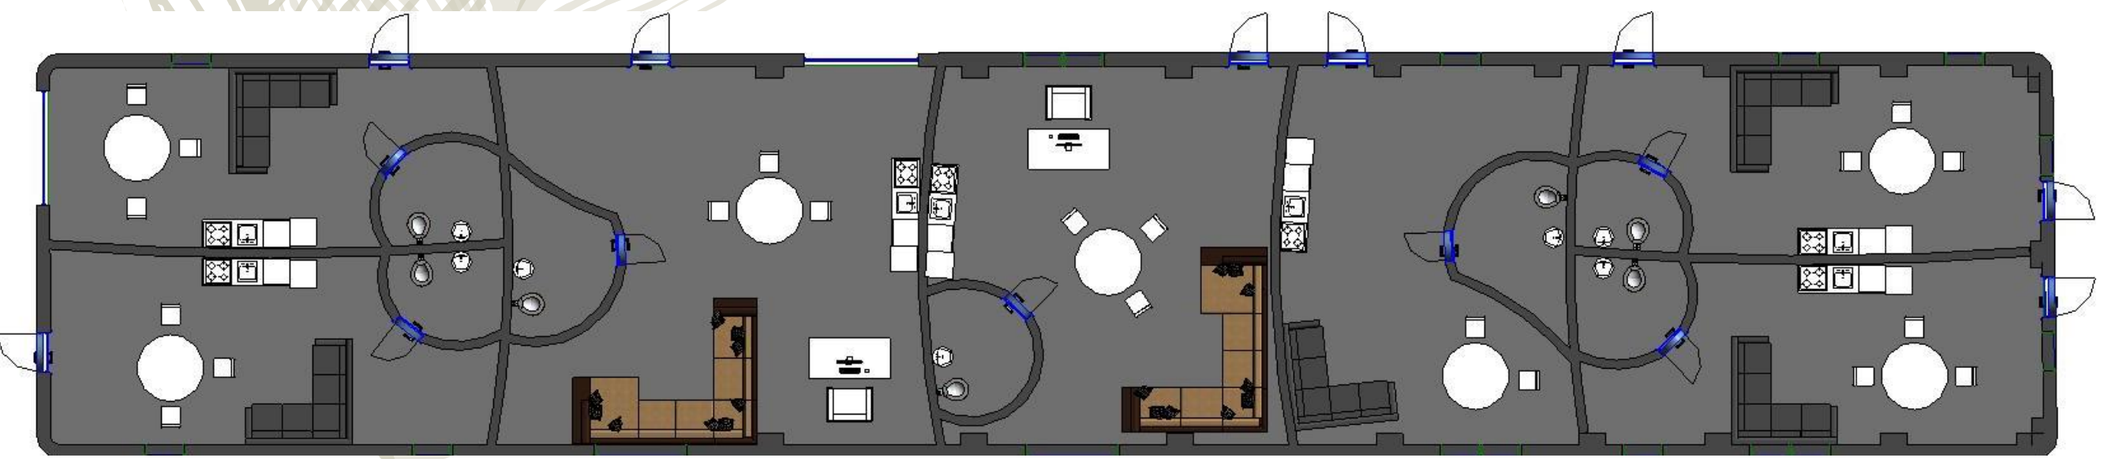

Building C (Artist Lofts)

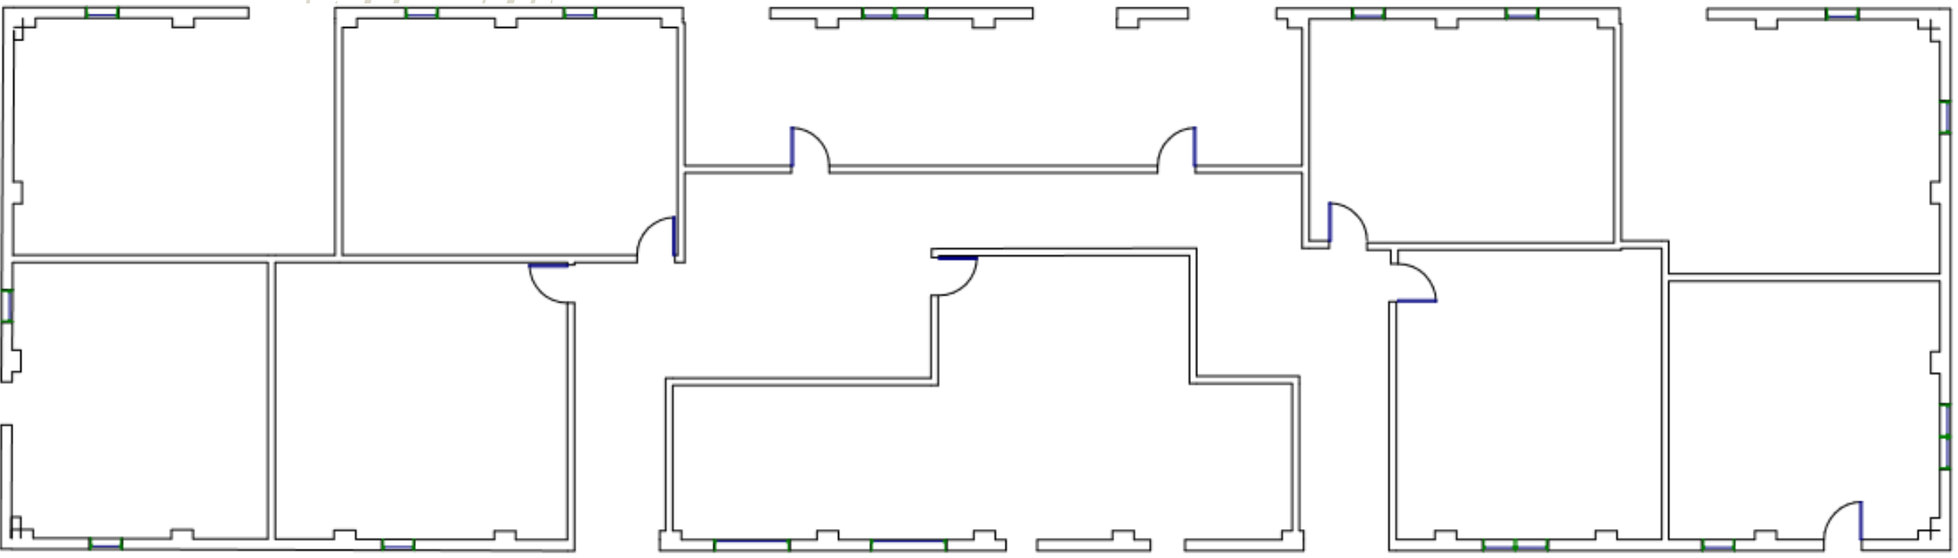

Building D (Artist Lofts) Process Documentation

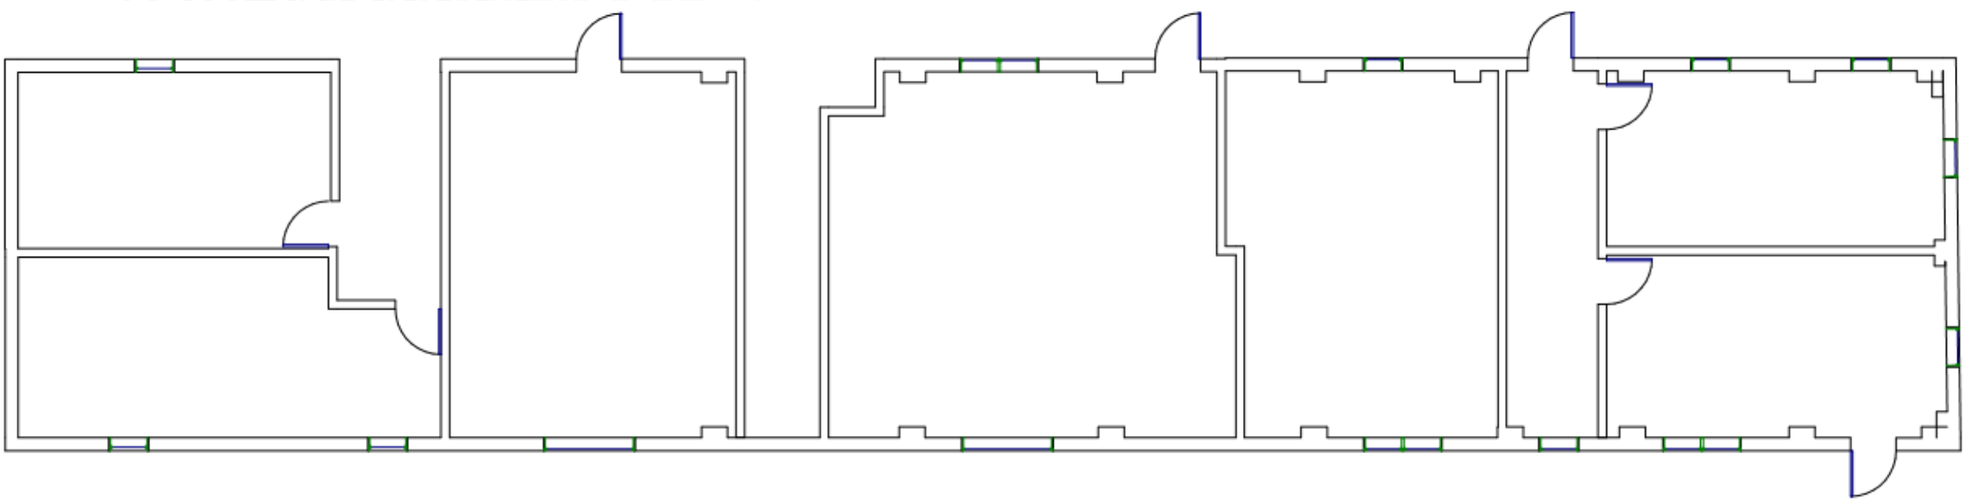

Building C (Artist Lofts) Process Documentation

NEXT Competition

The goal of this project is to design a space for the NEXT competition which includes multiple studios composed of diverse types of employees. Elements of curvature were added to create engaging design and coherent spatial connections.

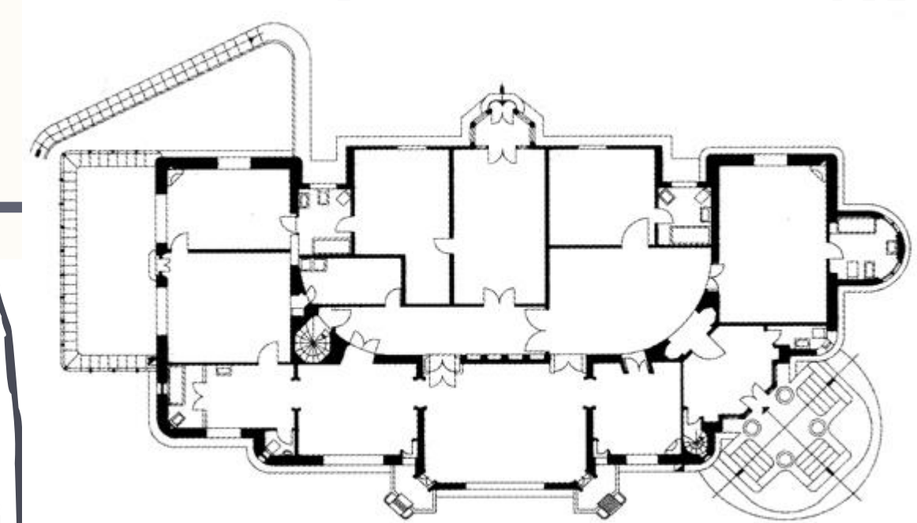

El Capricho - Gaudi

NEXT Competition Project

ID 4350 CAD II

Fall 2016

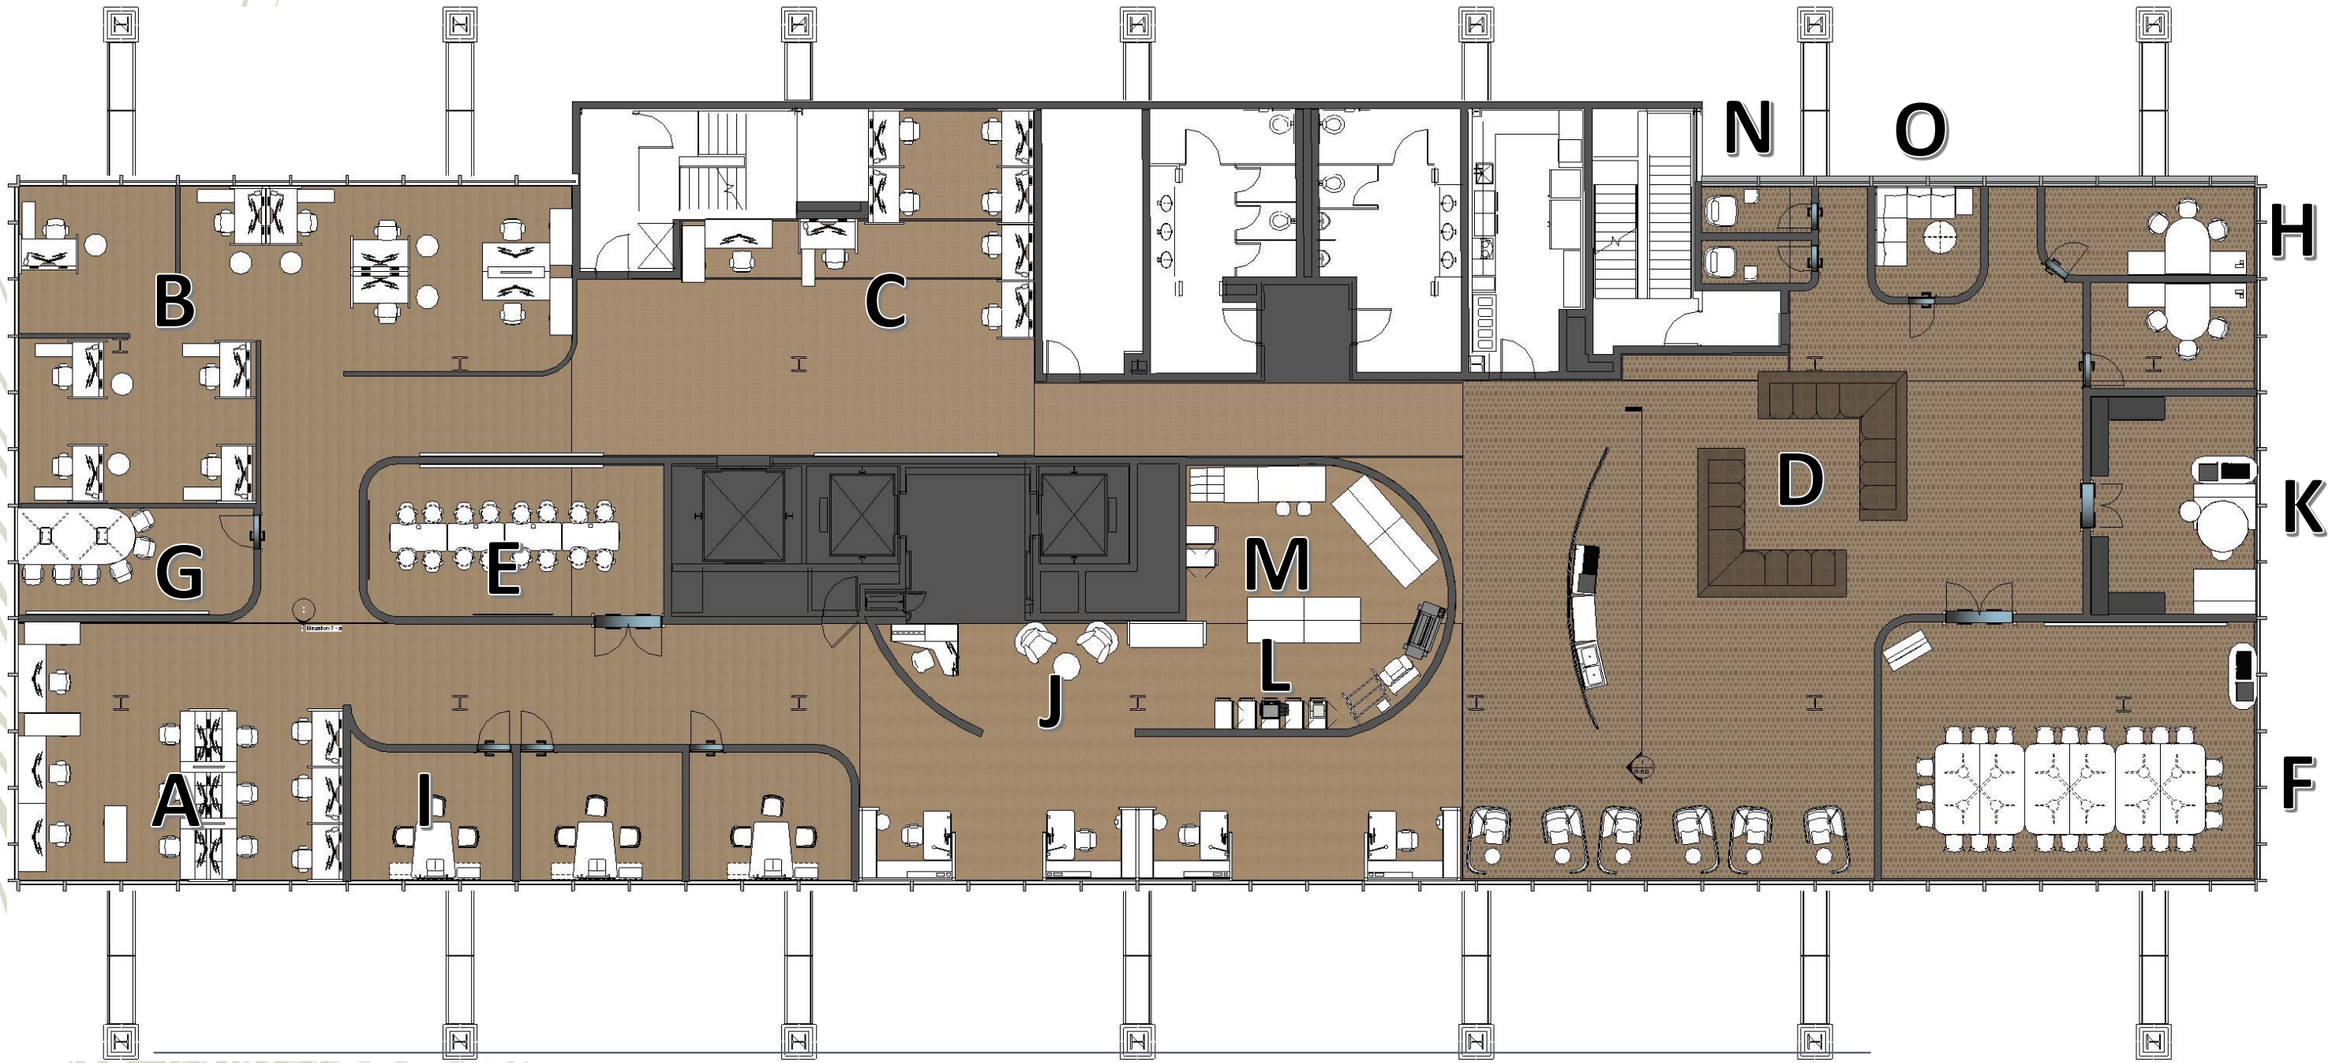

A. Education Studio	F. Large Conf.	K. Design Library
B. Corporate Studio	G. Medium Conf.	L. Resource Area
C. Healthcare Studio	H. Small Conf.	M. Model Space
D. Work café	I. Private Office	N. Quiet Rooms
E. BIM/VR/Training Room	J. Reception	O. Relax/Mother's Room

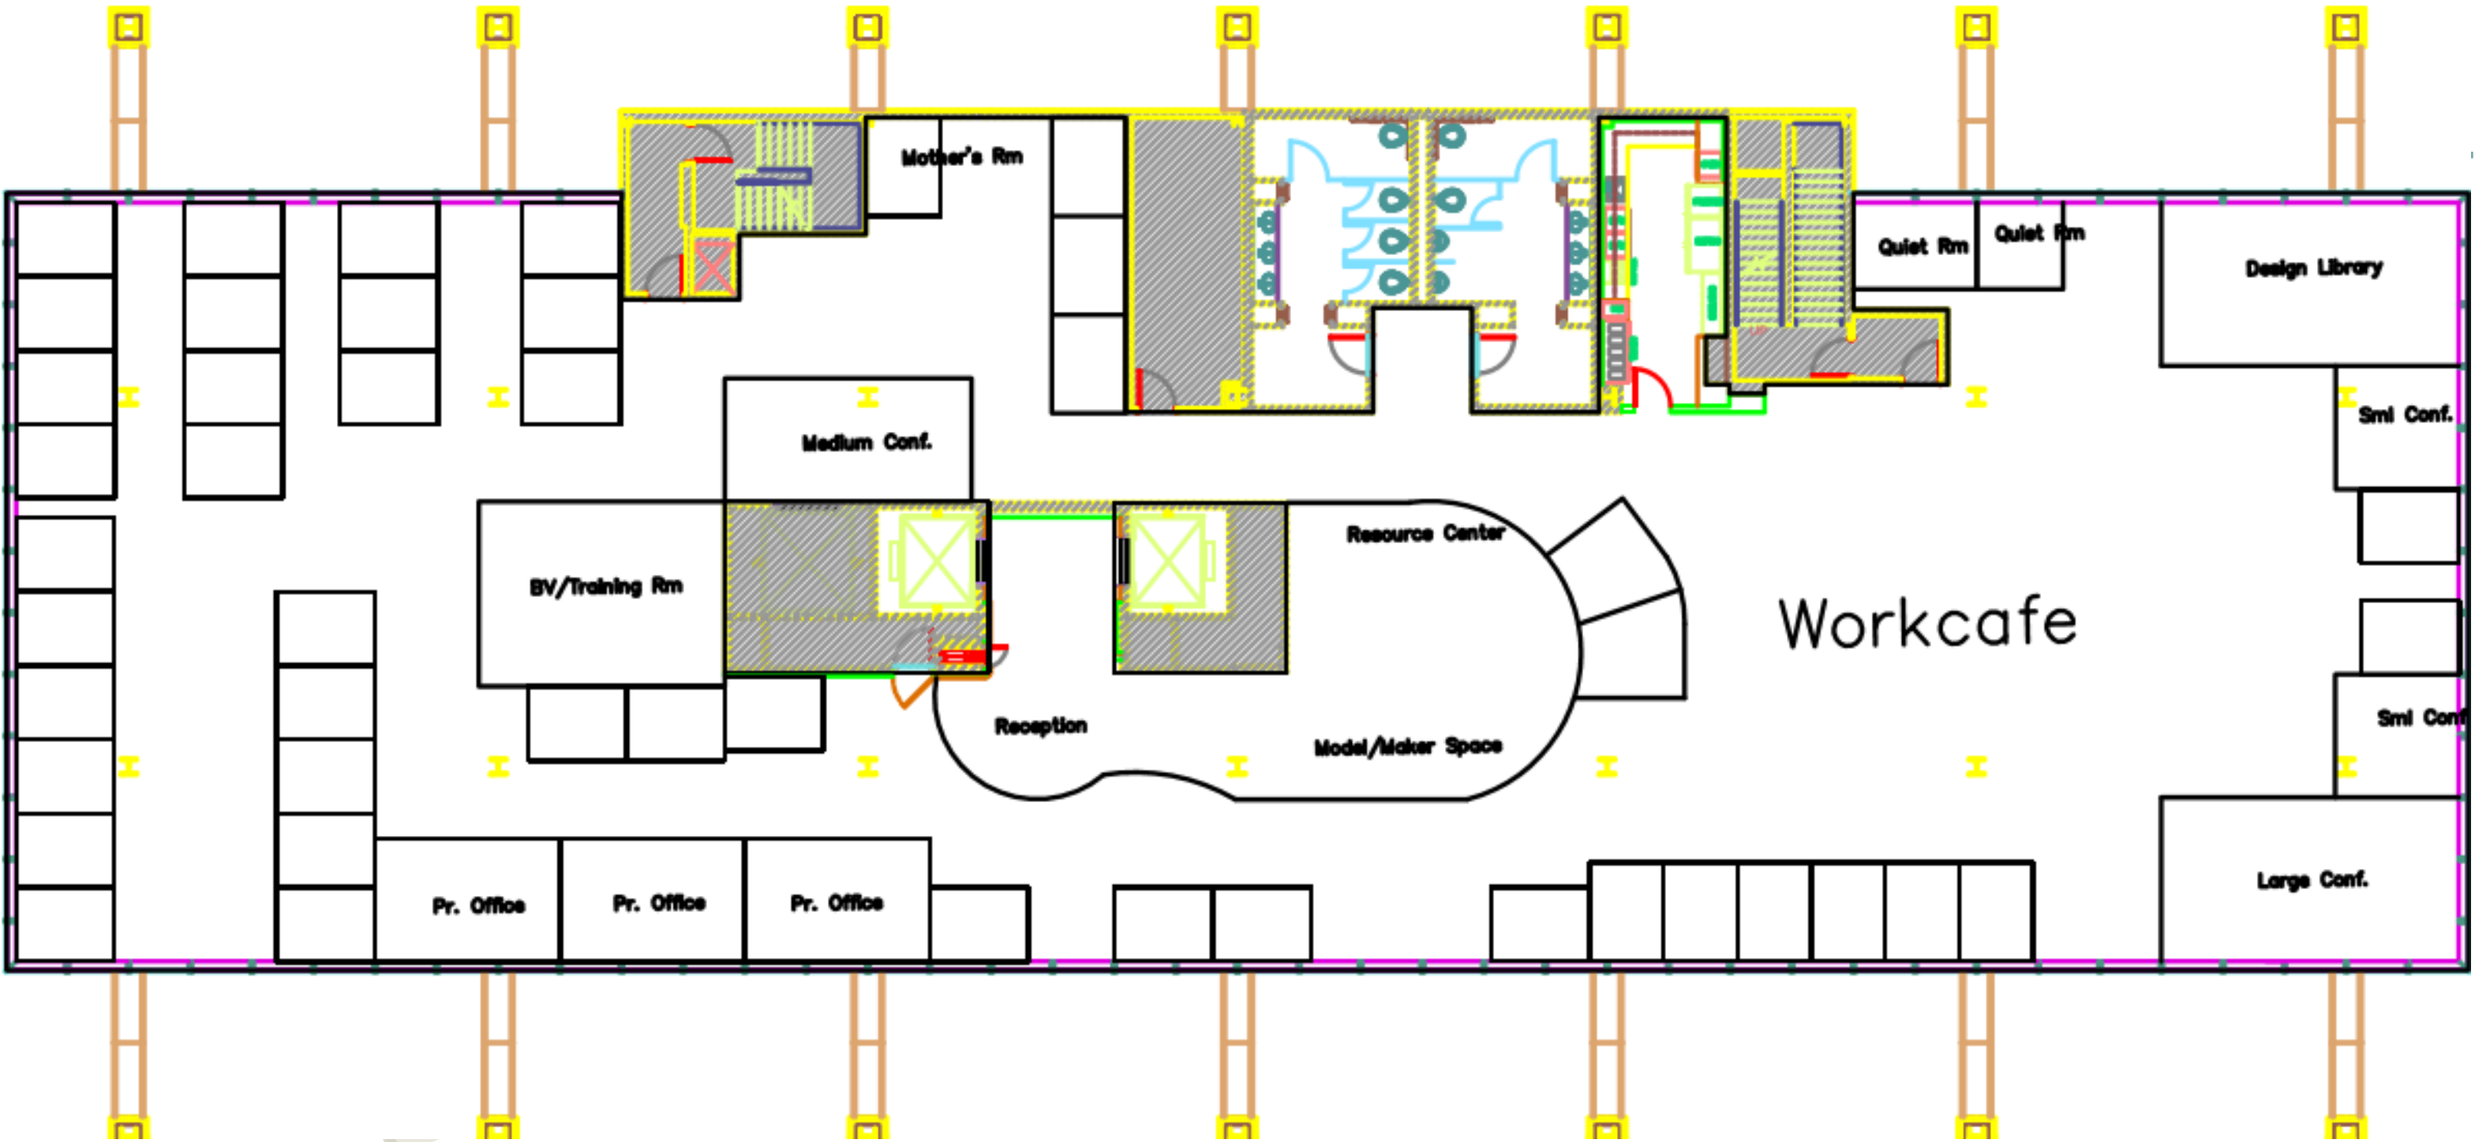

Floor Plan Process Documentation

NEXT Competition Project

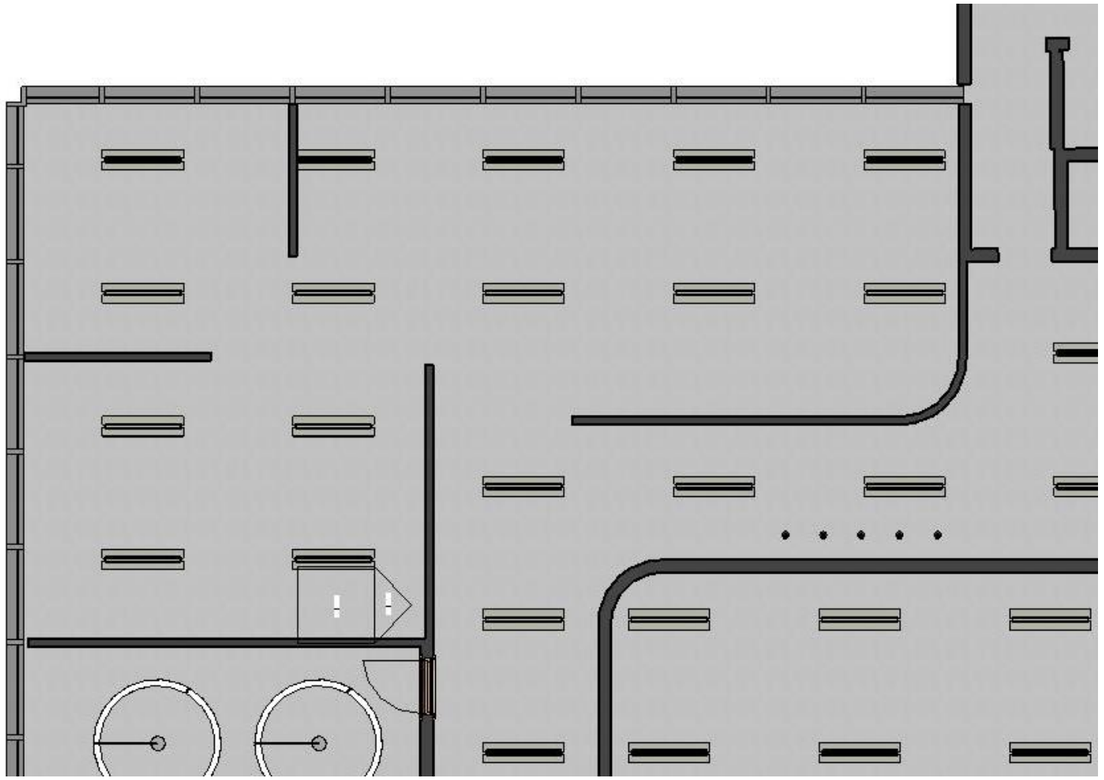

Corporate Studio RCP

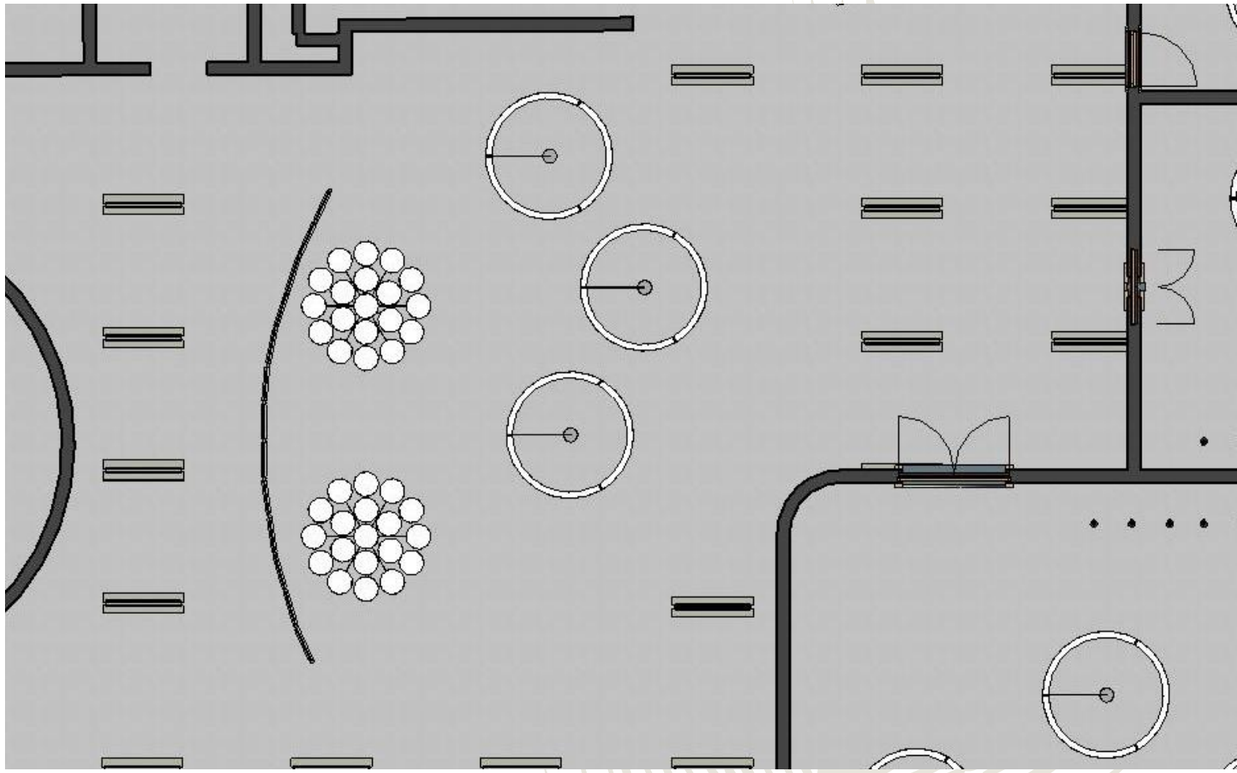

Workcafe RCP

Selux
Aura

Eureka Bouqet
Mika

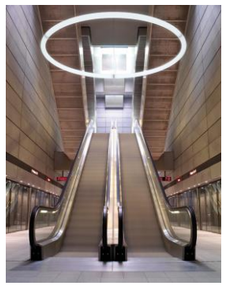

Eureka
Odeon

Turnstone
Big Lamp

NEXT Competition Project

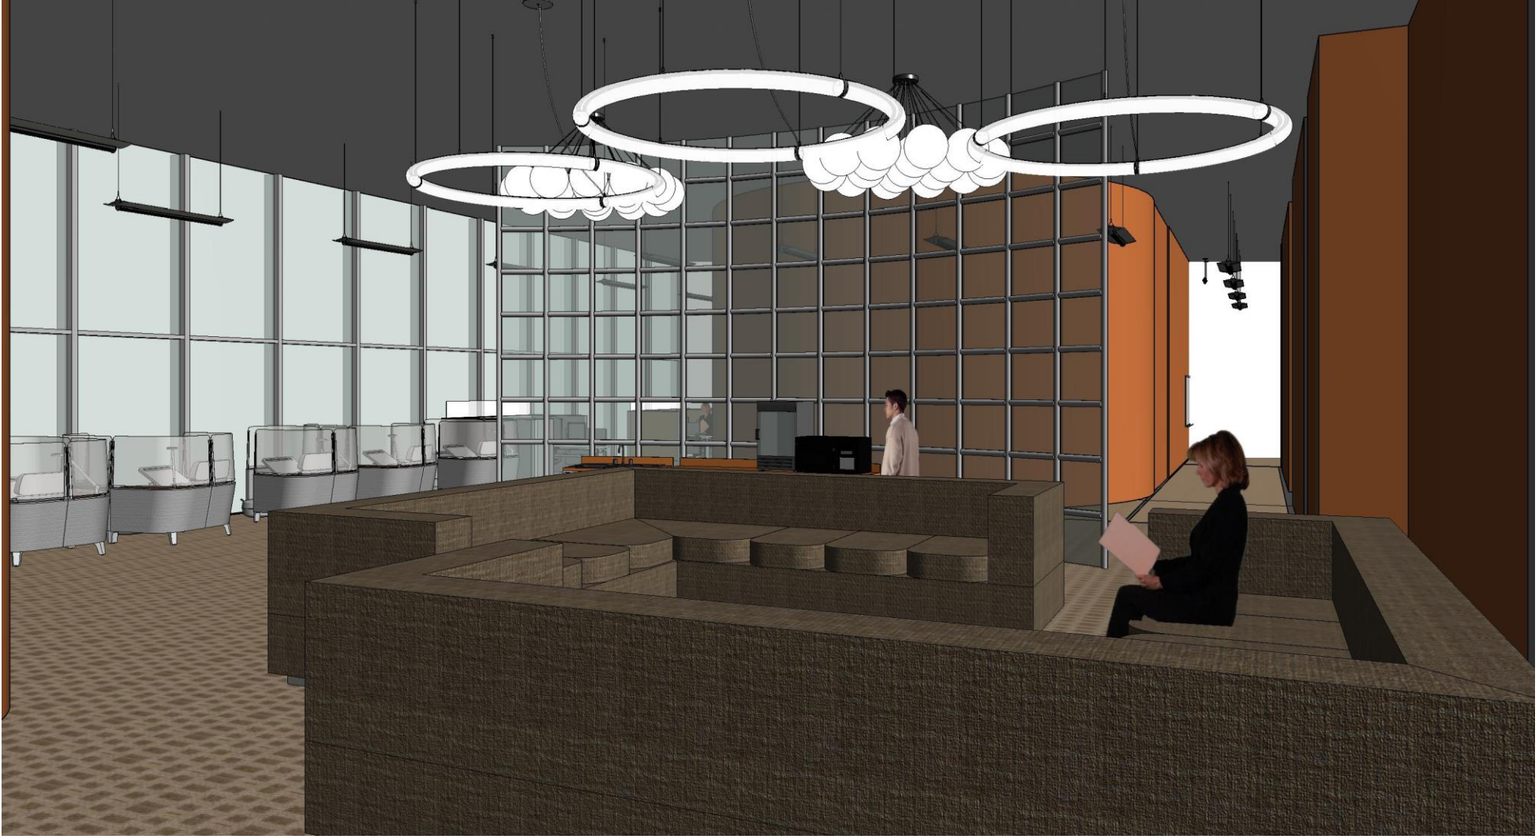

Workcafe Perspective

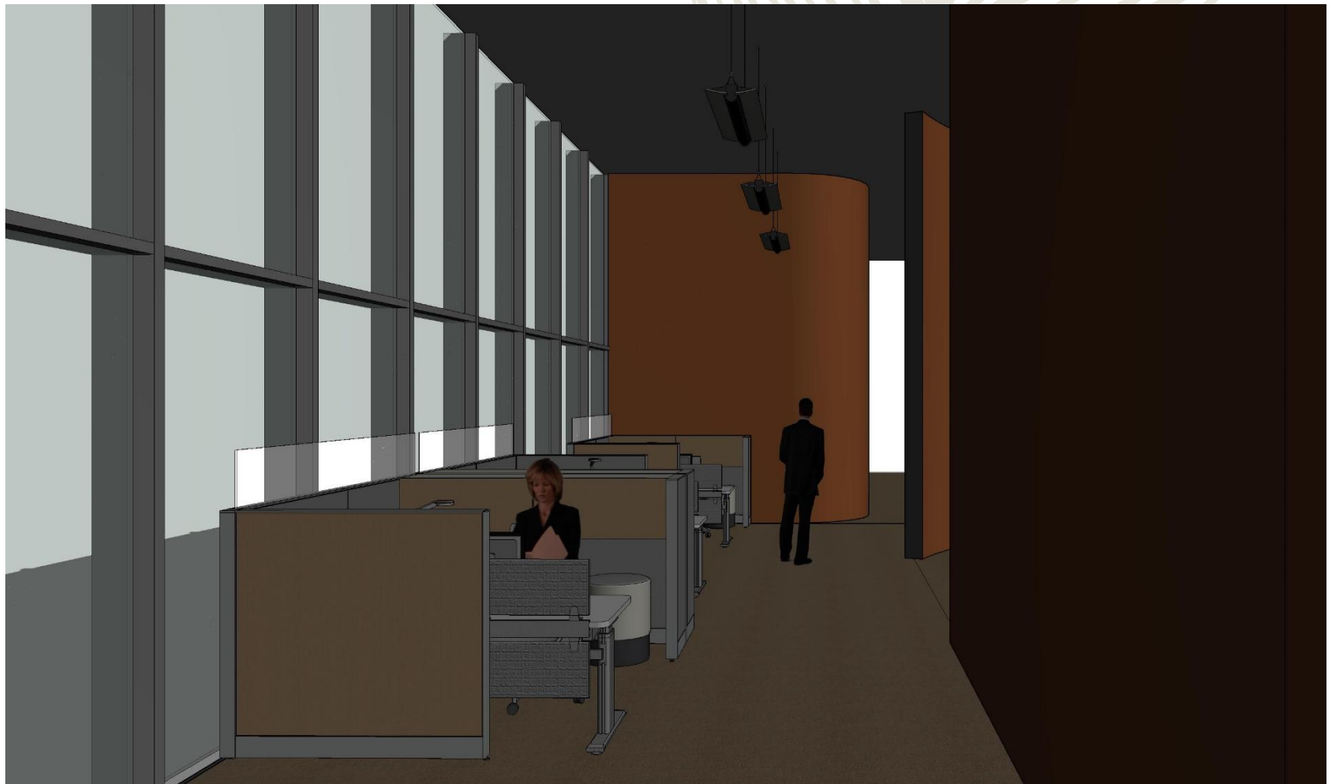

Reception Hallway Perspective

NEXT Competition Project

Education Studio Section

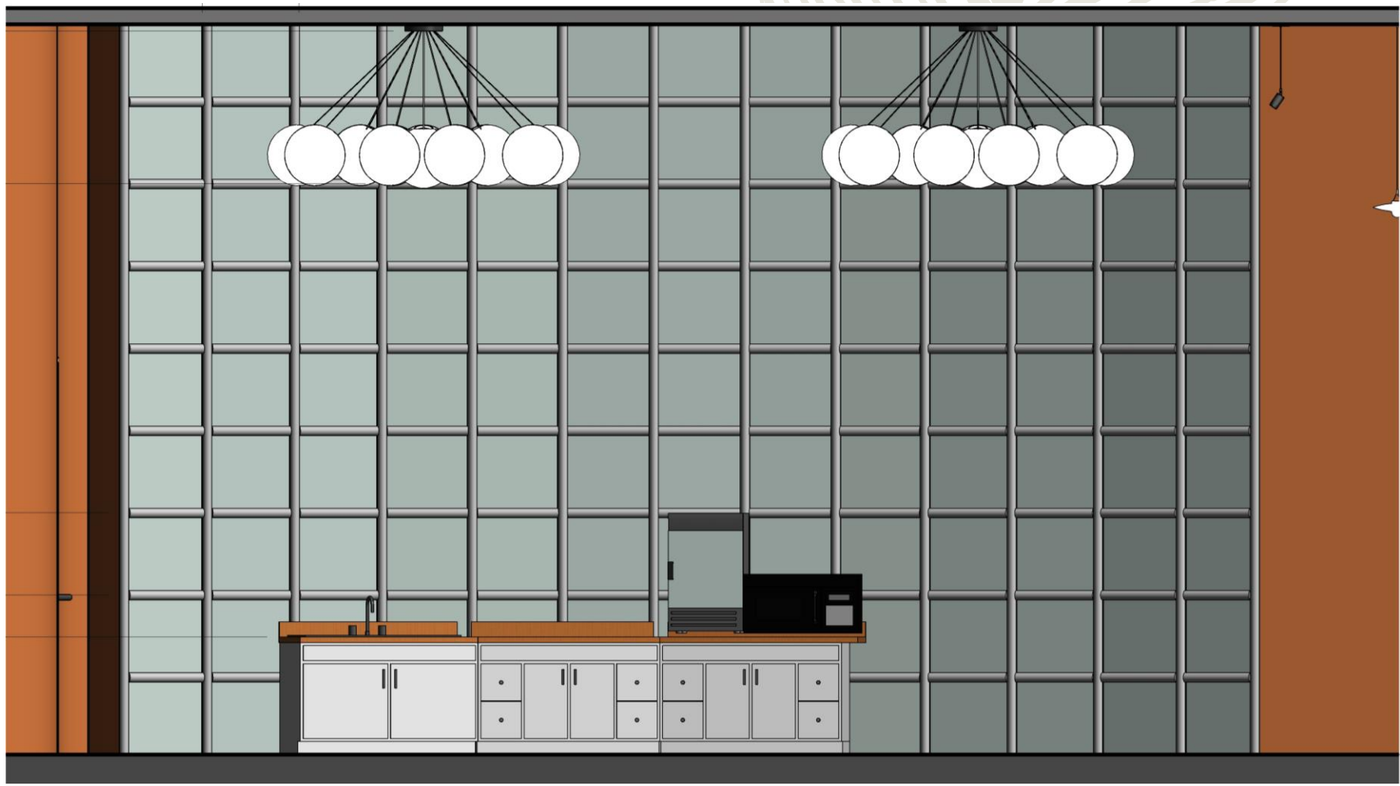

Workcafe Kitchen Section

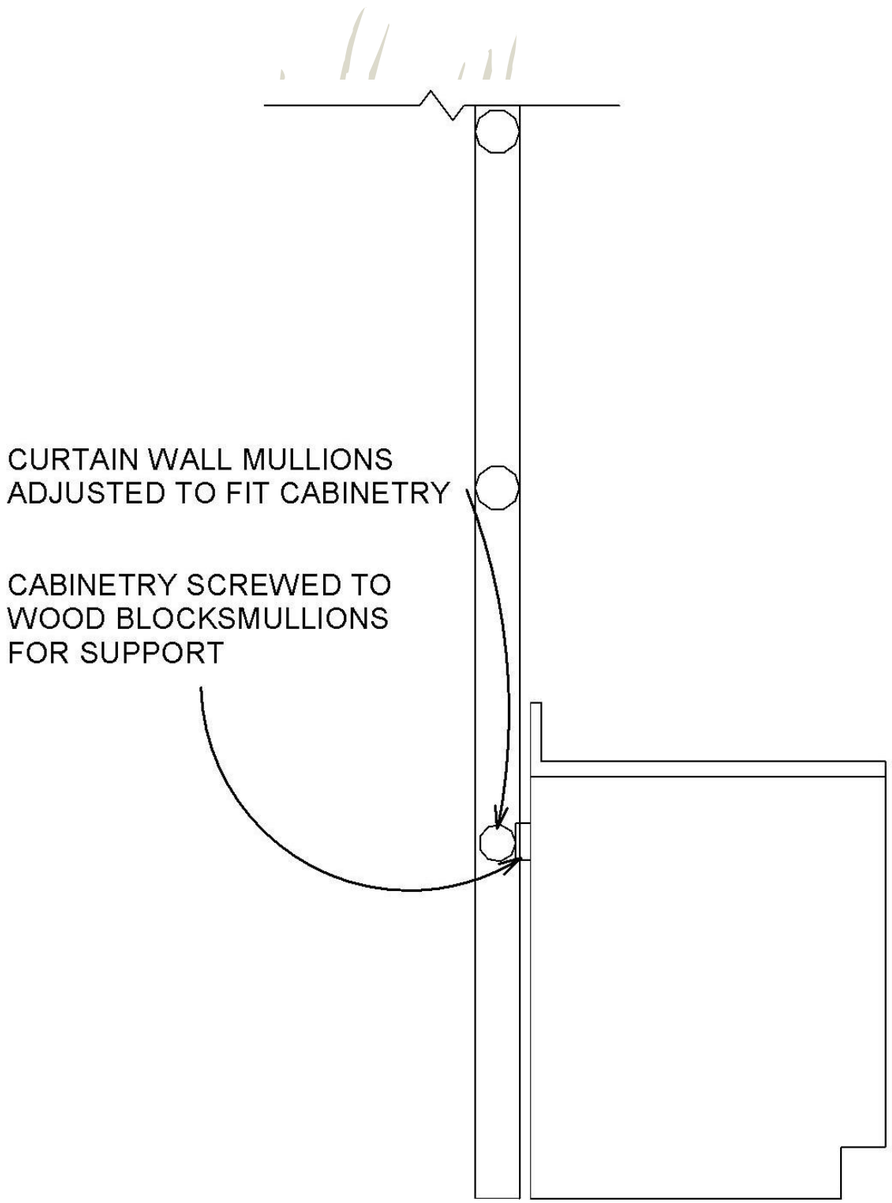

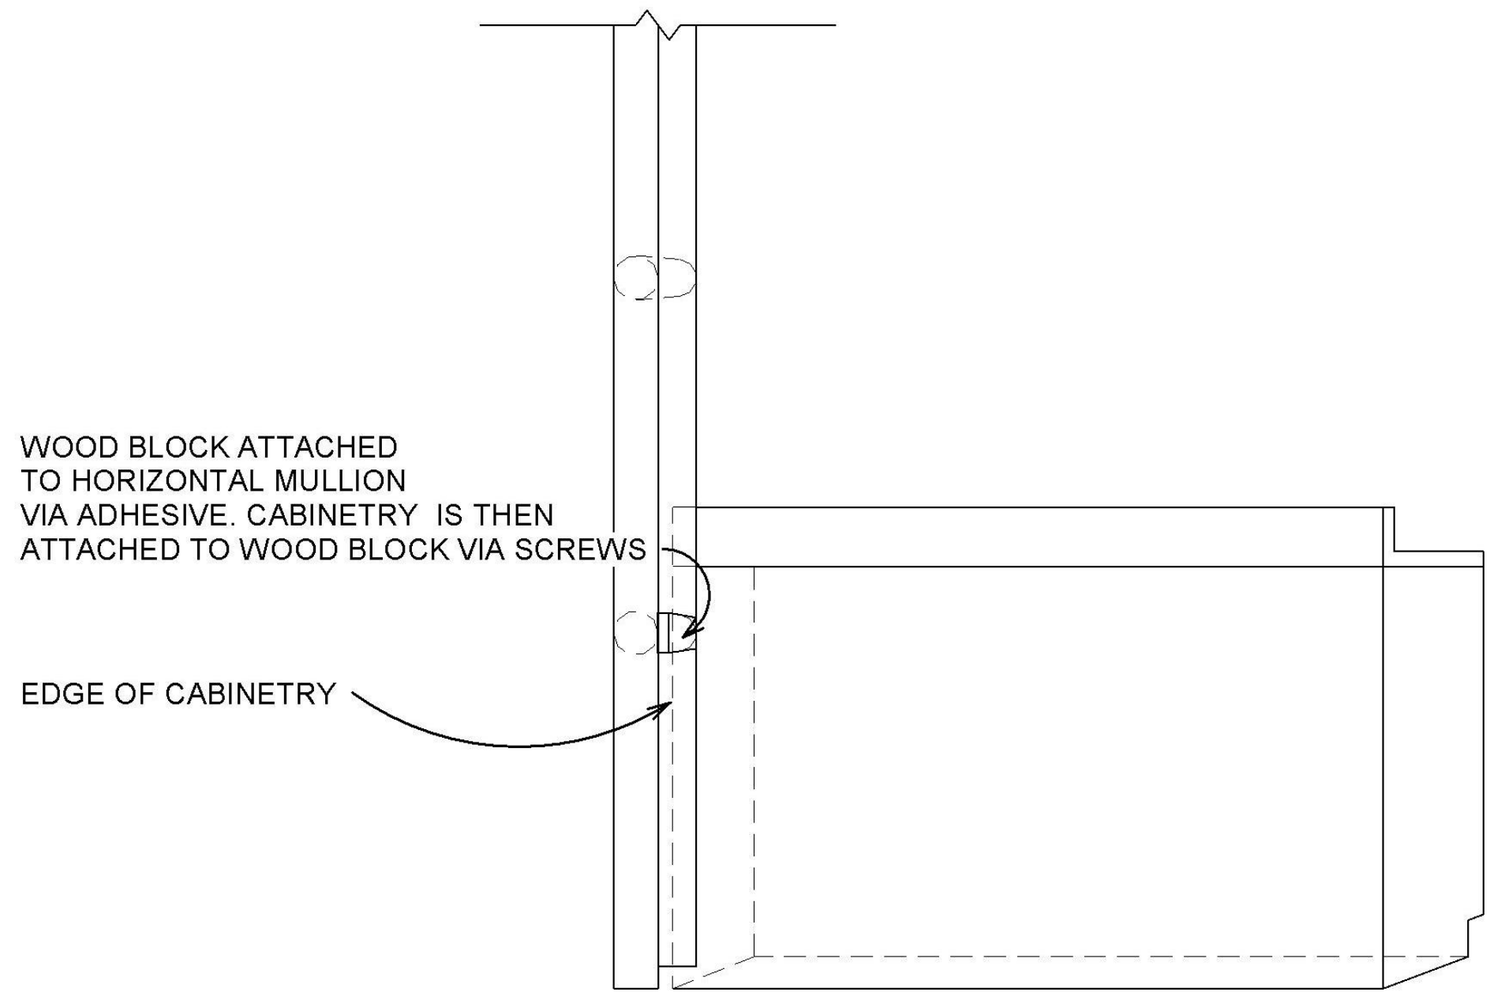

Cabinetry-Curtain Wall Connection

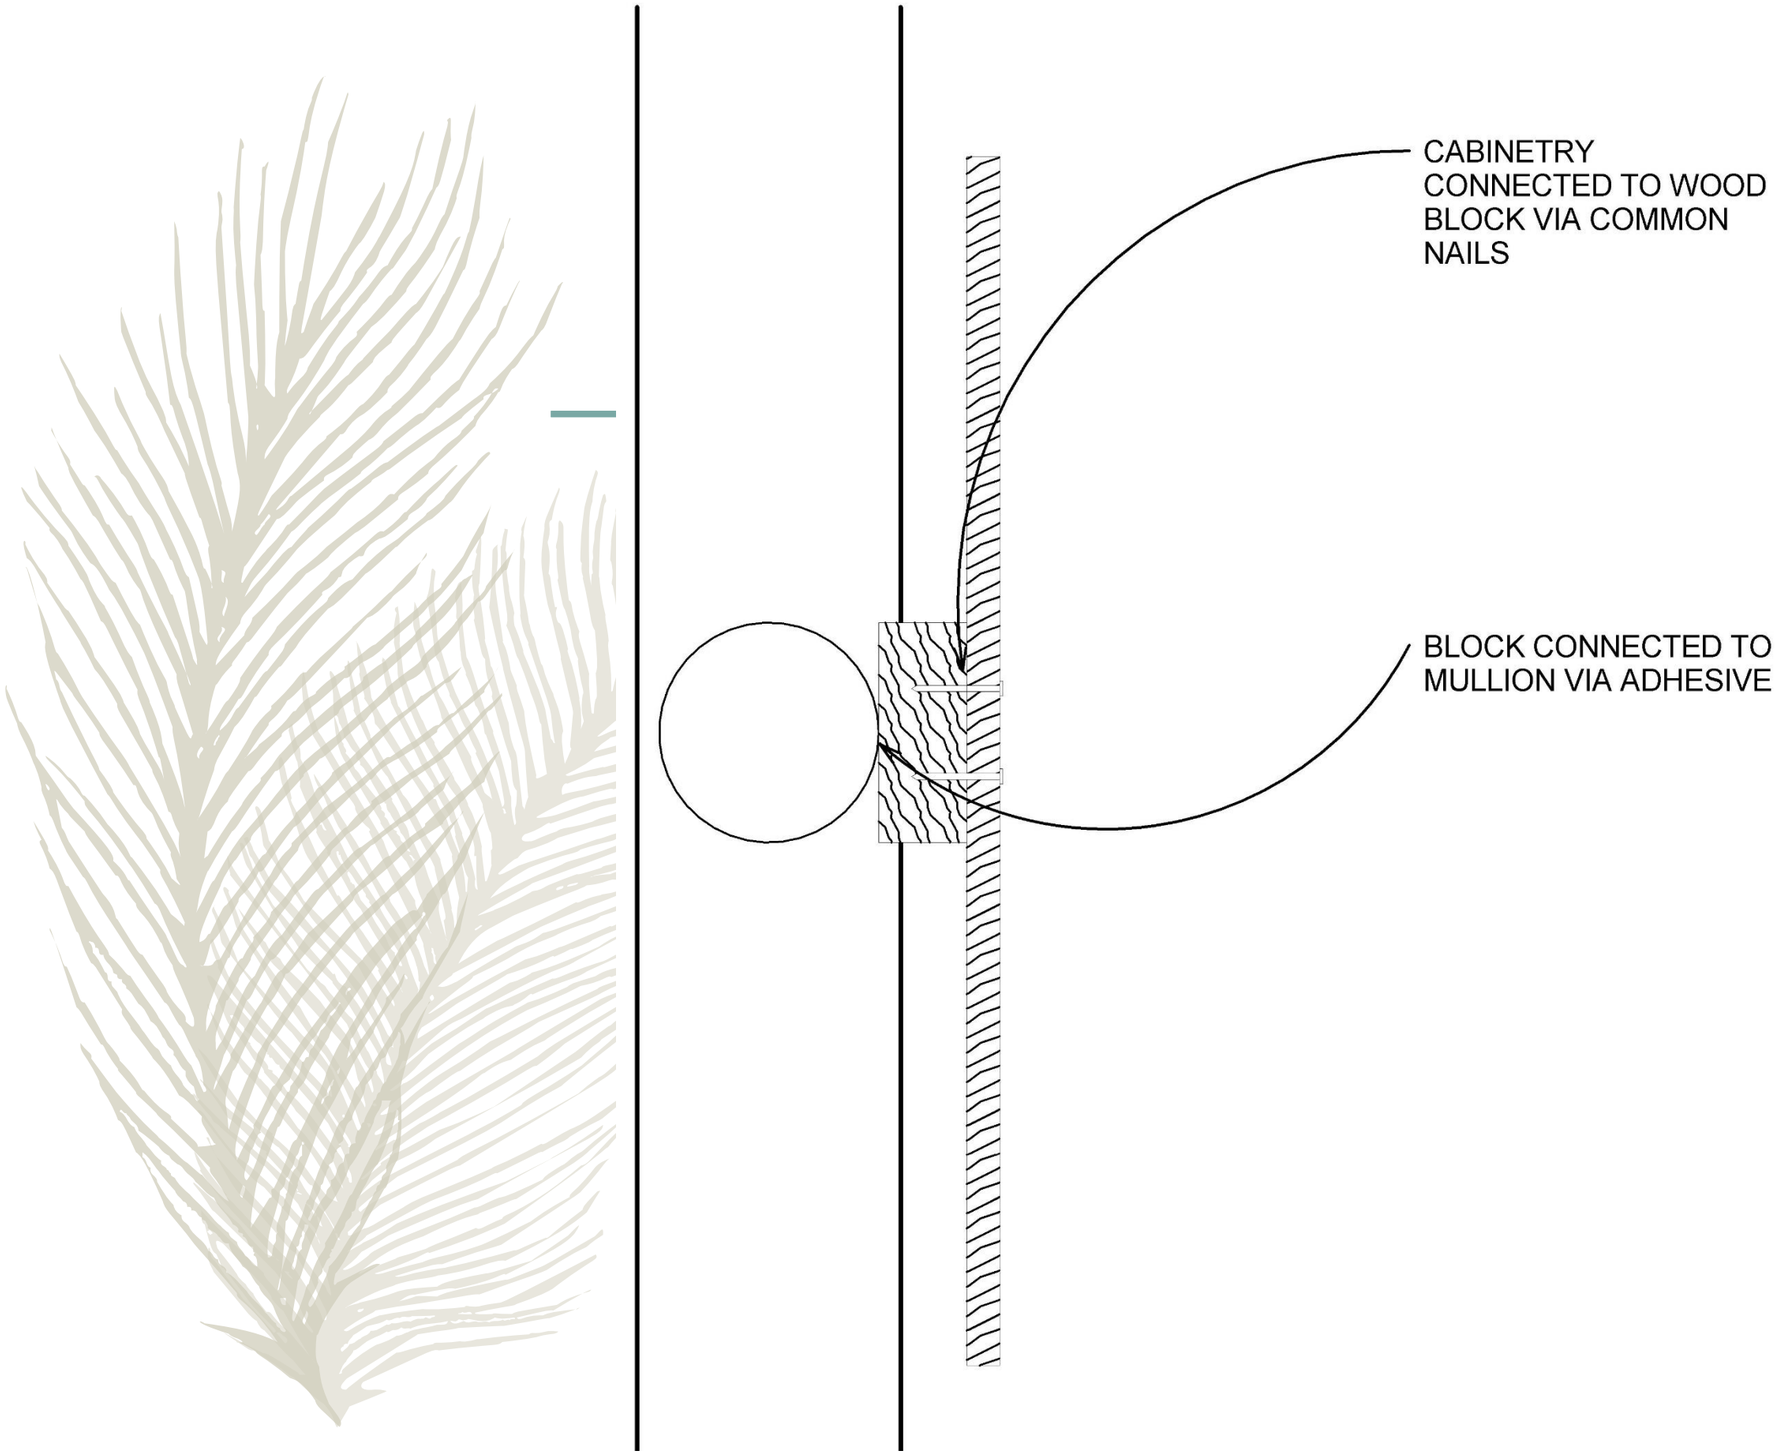

Cabinetry-Curtain Wall Connection

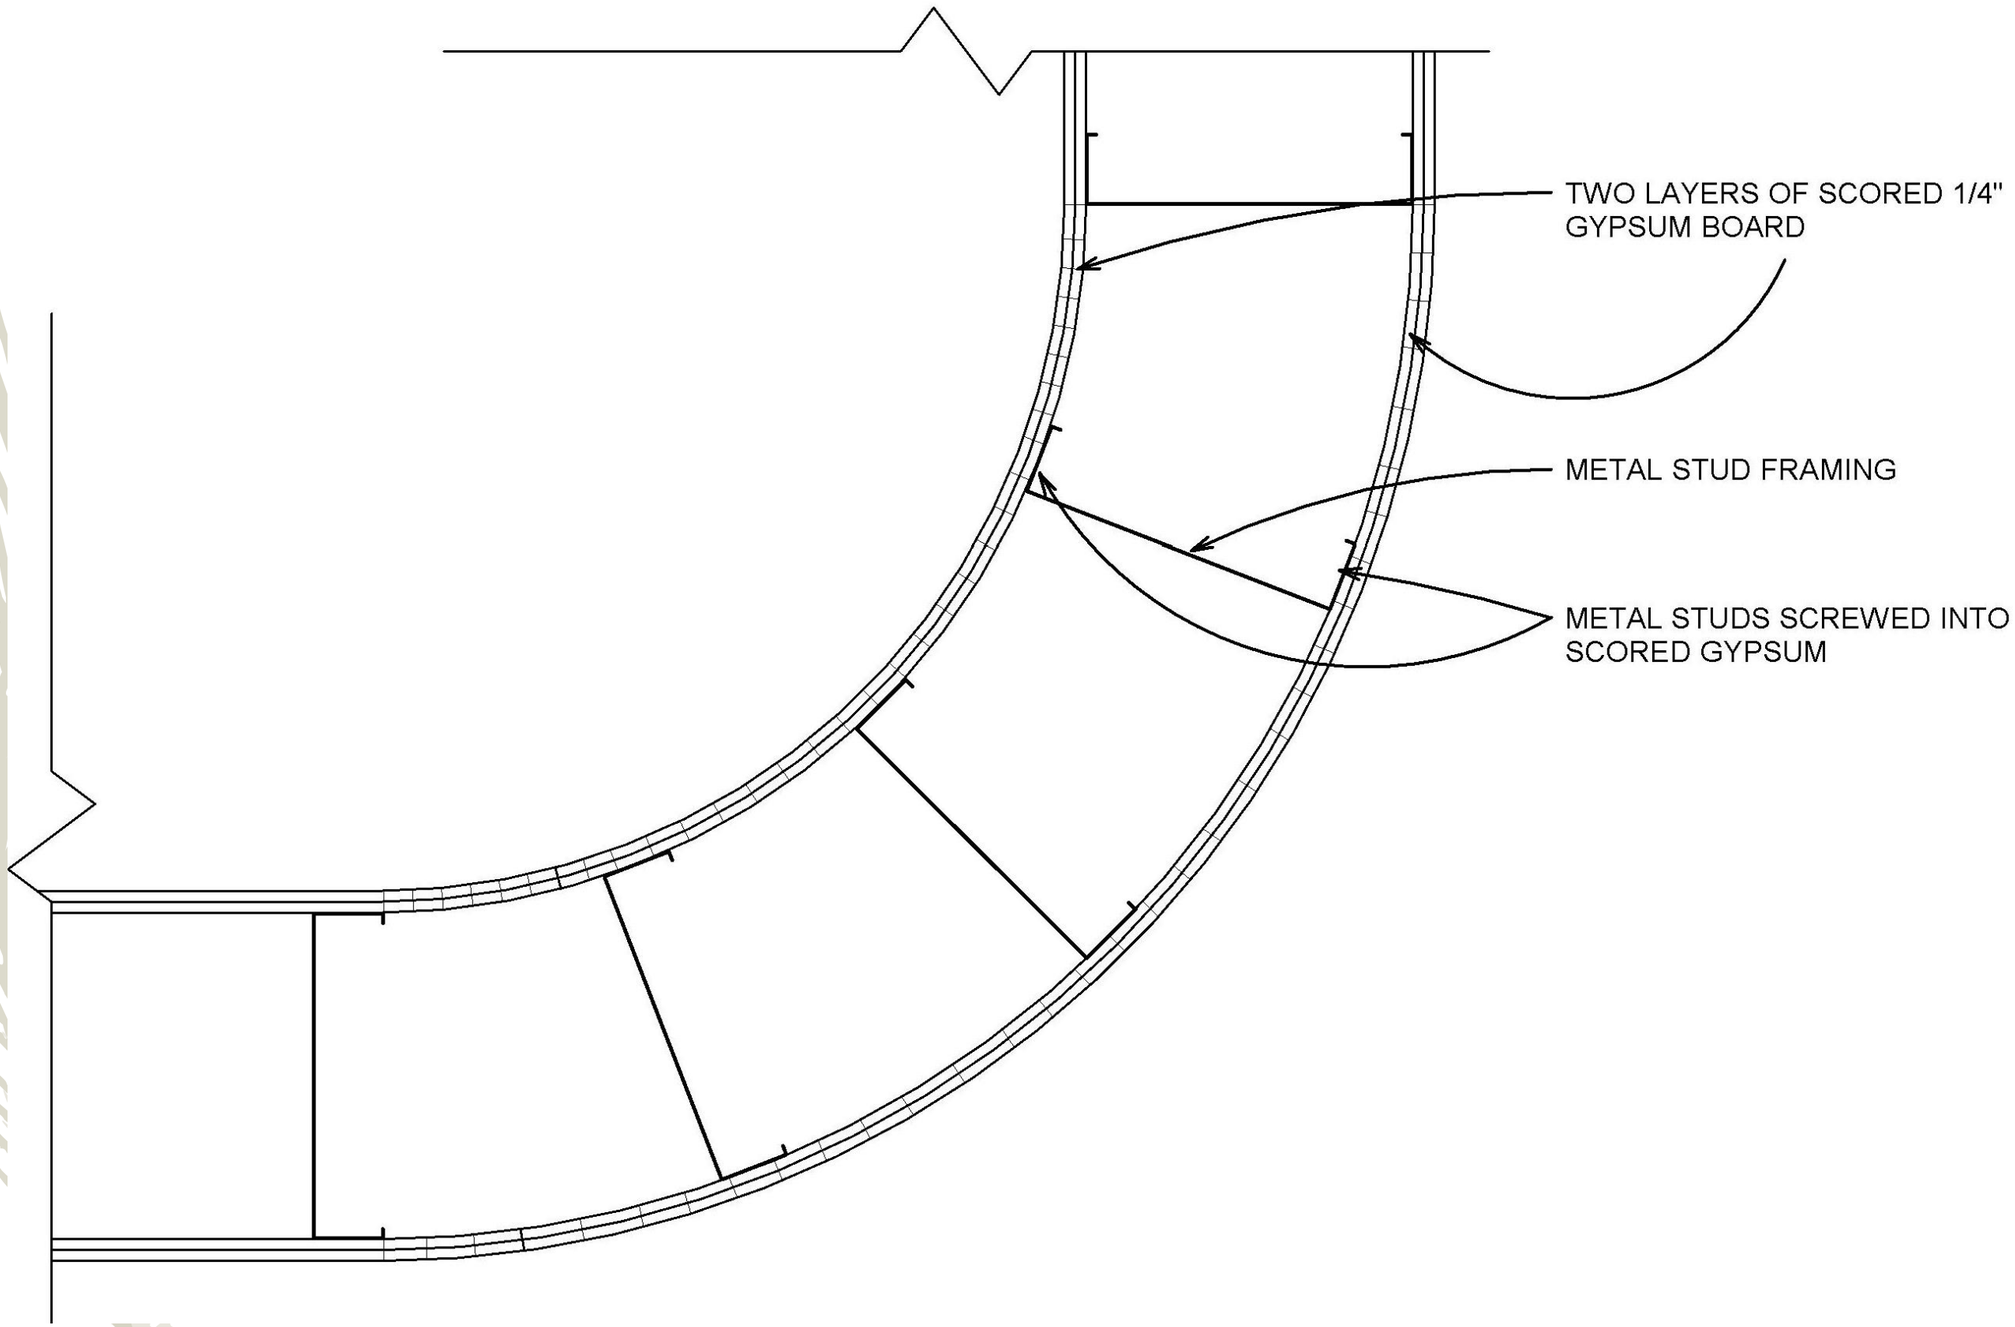

Curved Wall Detail

150 Nassau Street, Manhattan, New York

The goal of this apartment design is to illustrate sufficient space allotment for a social, yet work-focused single individual. Following this reasoning, more space is given to the living room and kitchen areas to accommodate guest. Considerations are taken to ensure the luxury of this design given the status of the area and cost of living in the apartment.

150 Nassau Street, Manhattan, New York
ID 4200 Residential Design
Spring 2017

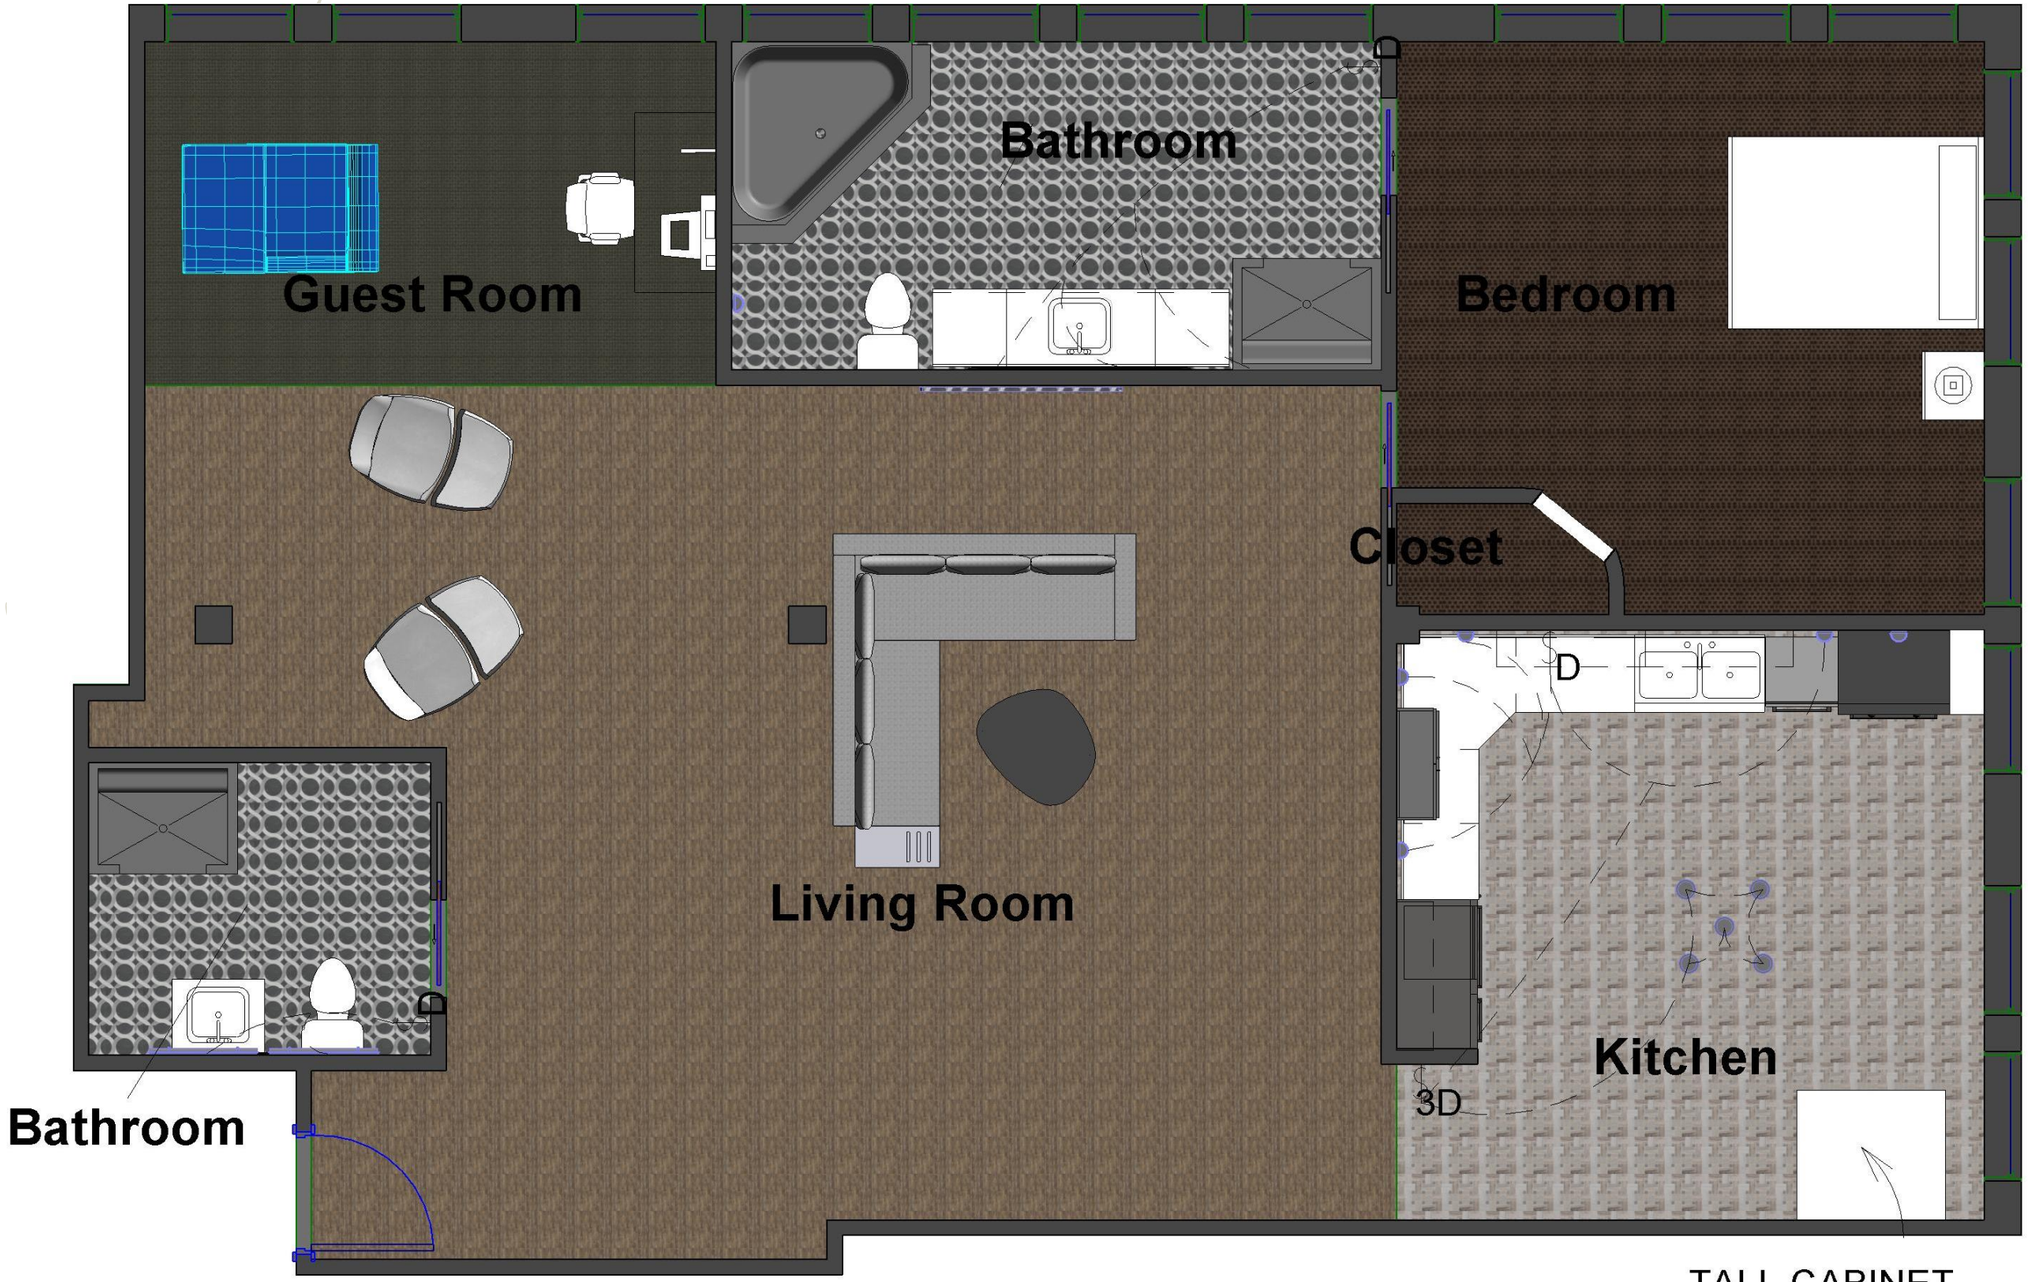

TALL CABINET
CONTAINING STACKED
WASHER AND DRYER

Apartment Floor Plan

150 Nassau Street, Manhattan, New York

Apartment Floor Plan Process Documentation

Reflected Ceiling Plan

150 Nassau Street, Manhattan, New York

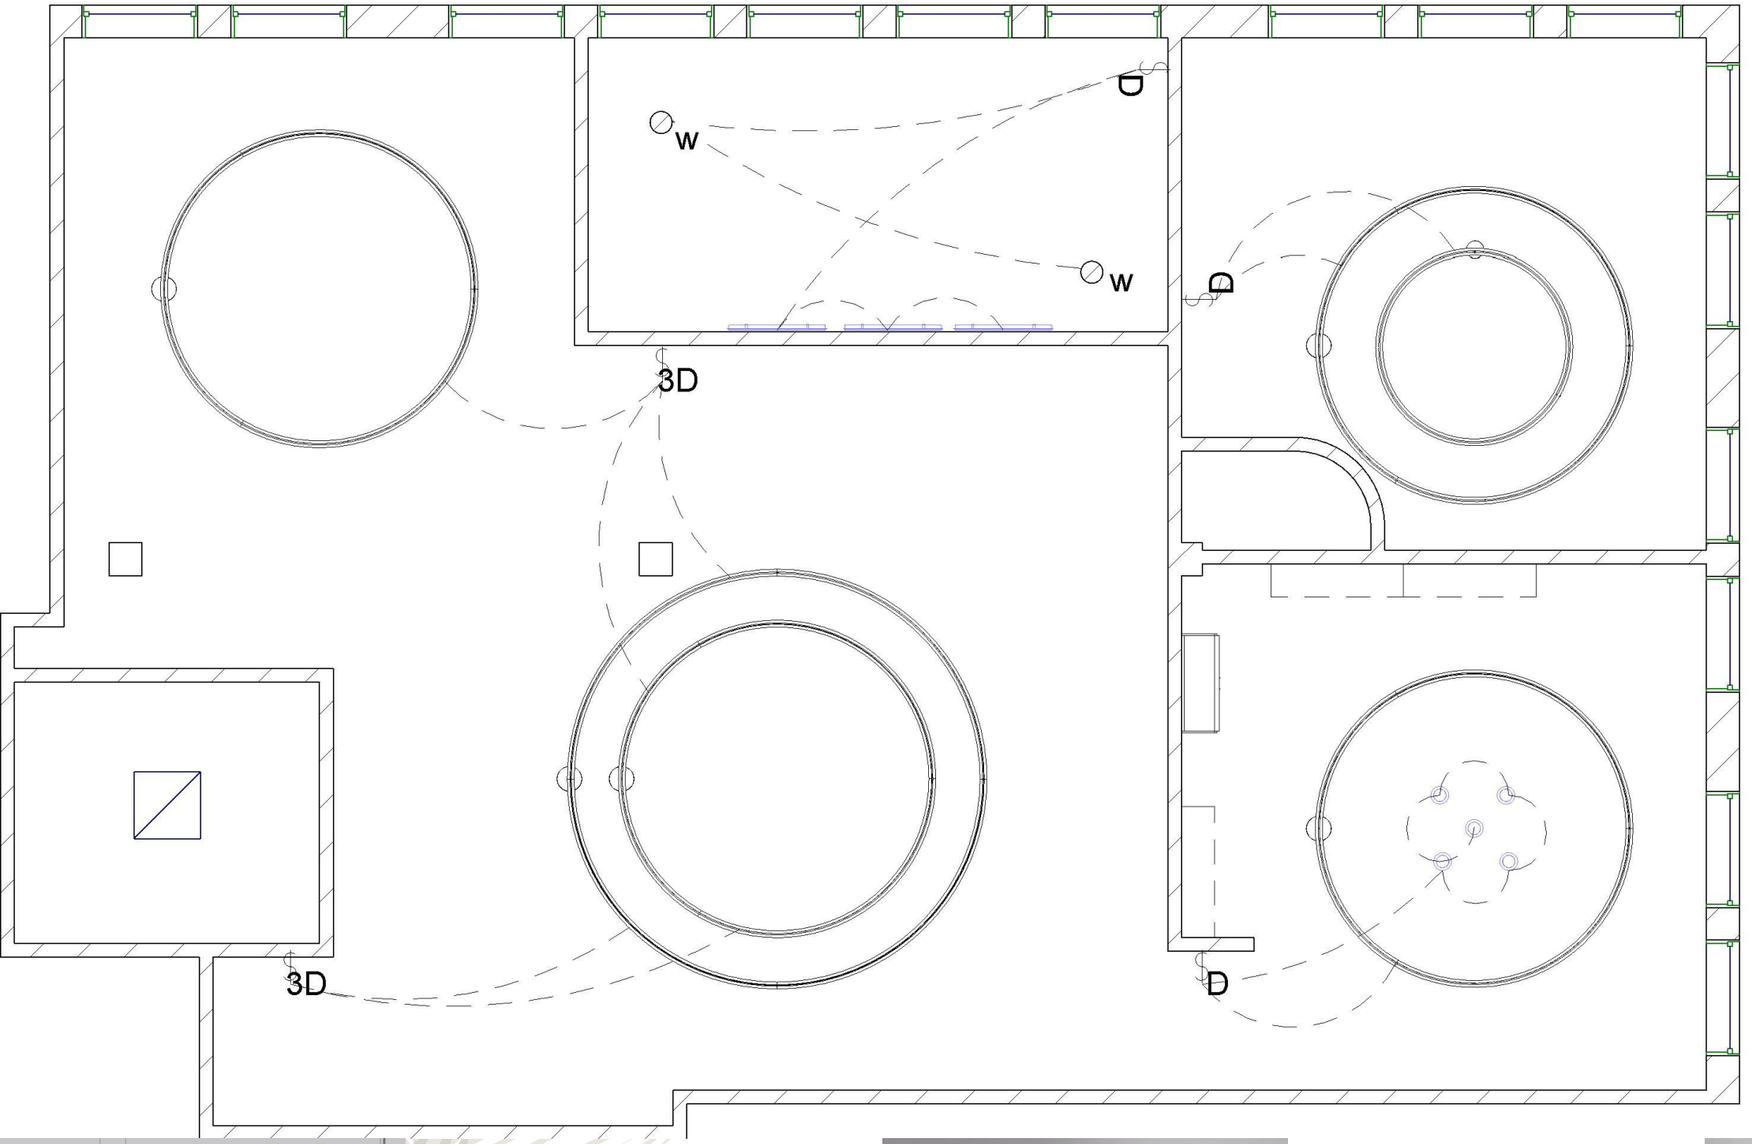

Eureka

Cycle

Waclighting

Elenentum

Waclighting

Vie

150 Nassau Street, Manhattan, New York

Living Room Perspective

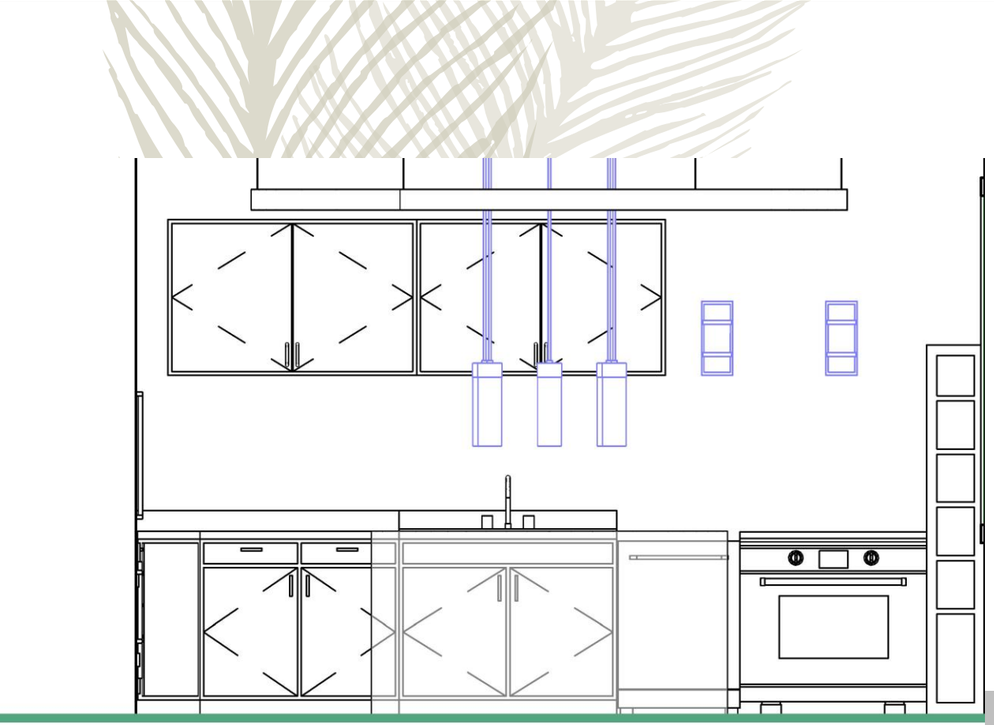

Kitchen Elevation

Master Bathroom Elevation

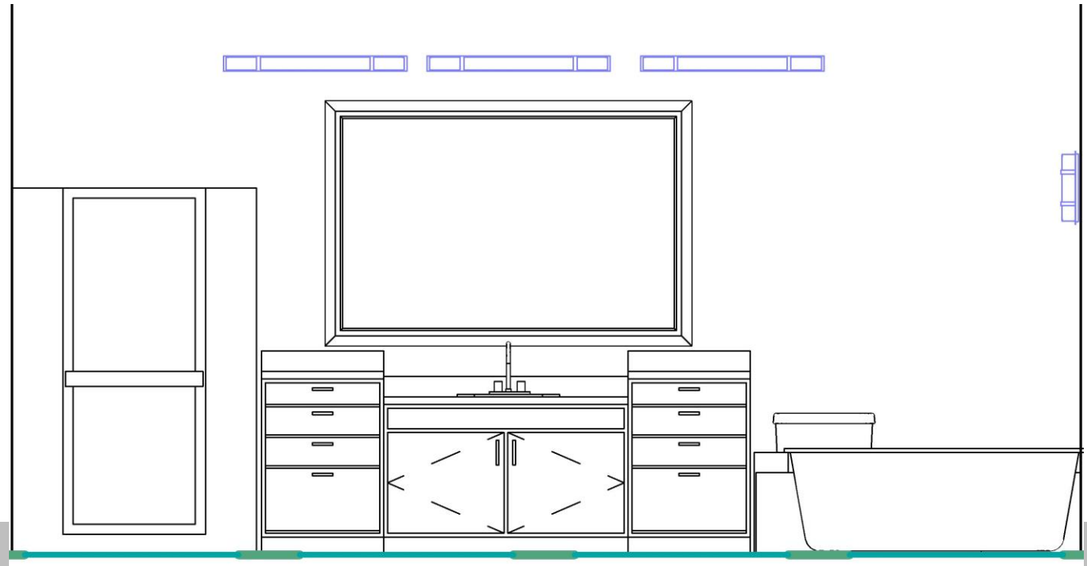

Intern work done for Pedini Atlanta/Lee Bryan Interior Design

Pedini Atlanta and Lee Bryan Interior Design both operate from the Pedini showroom in ADAC located in Atlanta. The Pedini portion deals with kitchen design and the LBID portion deals with commercial and residential projects.

Intern Work from Pedini Atlanta/LBID
Summer 2017

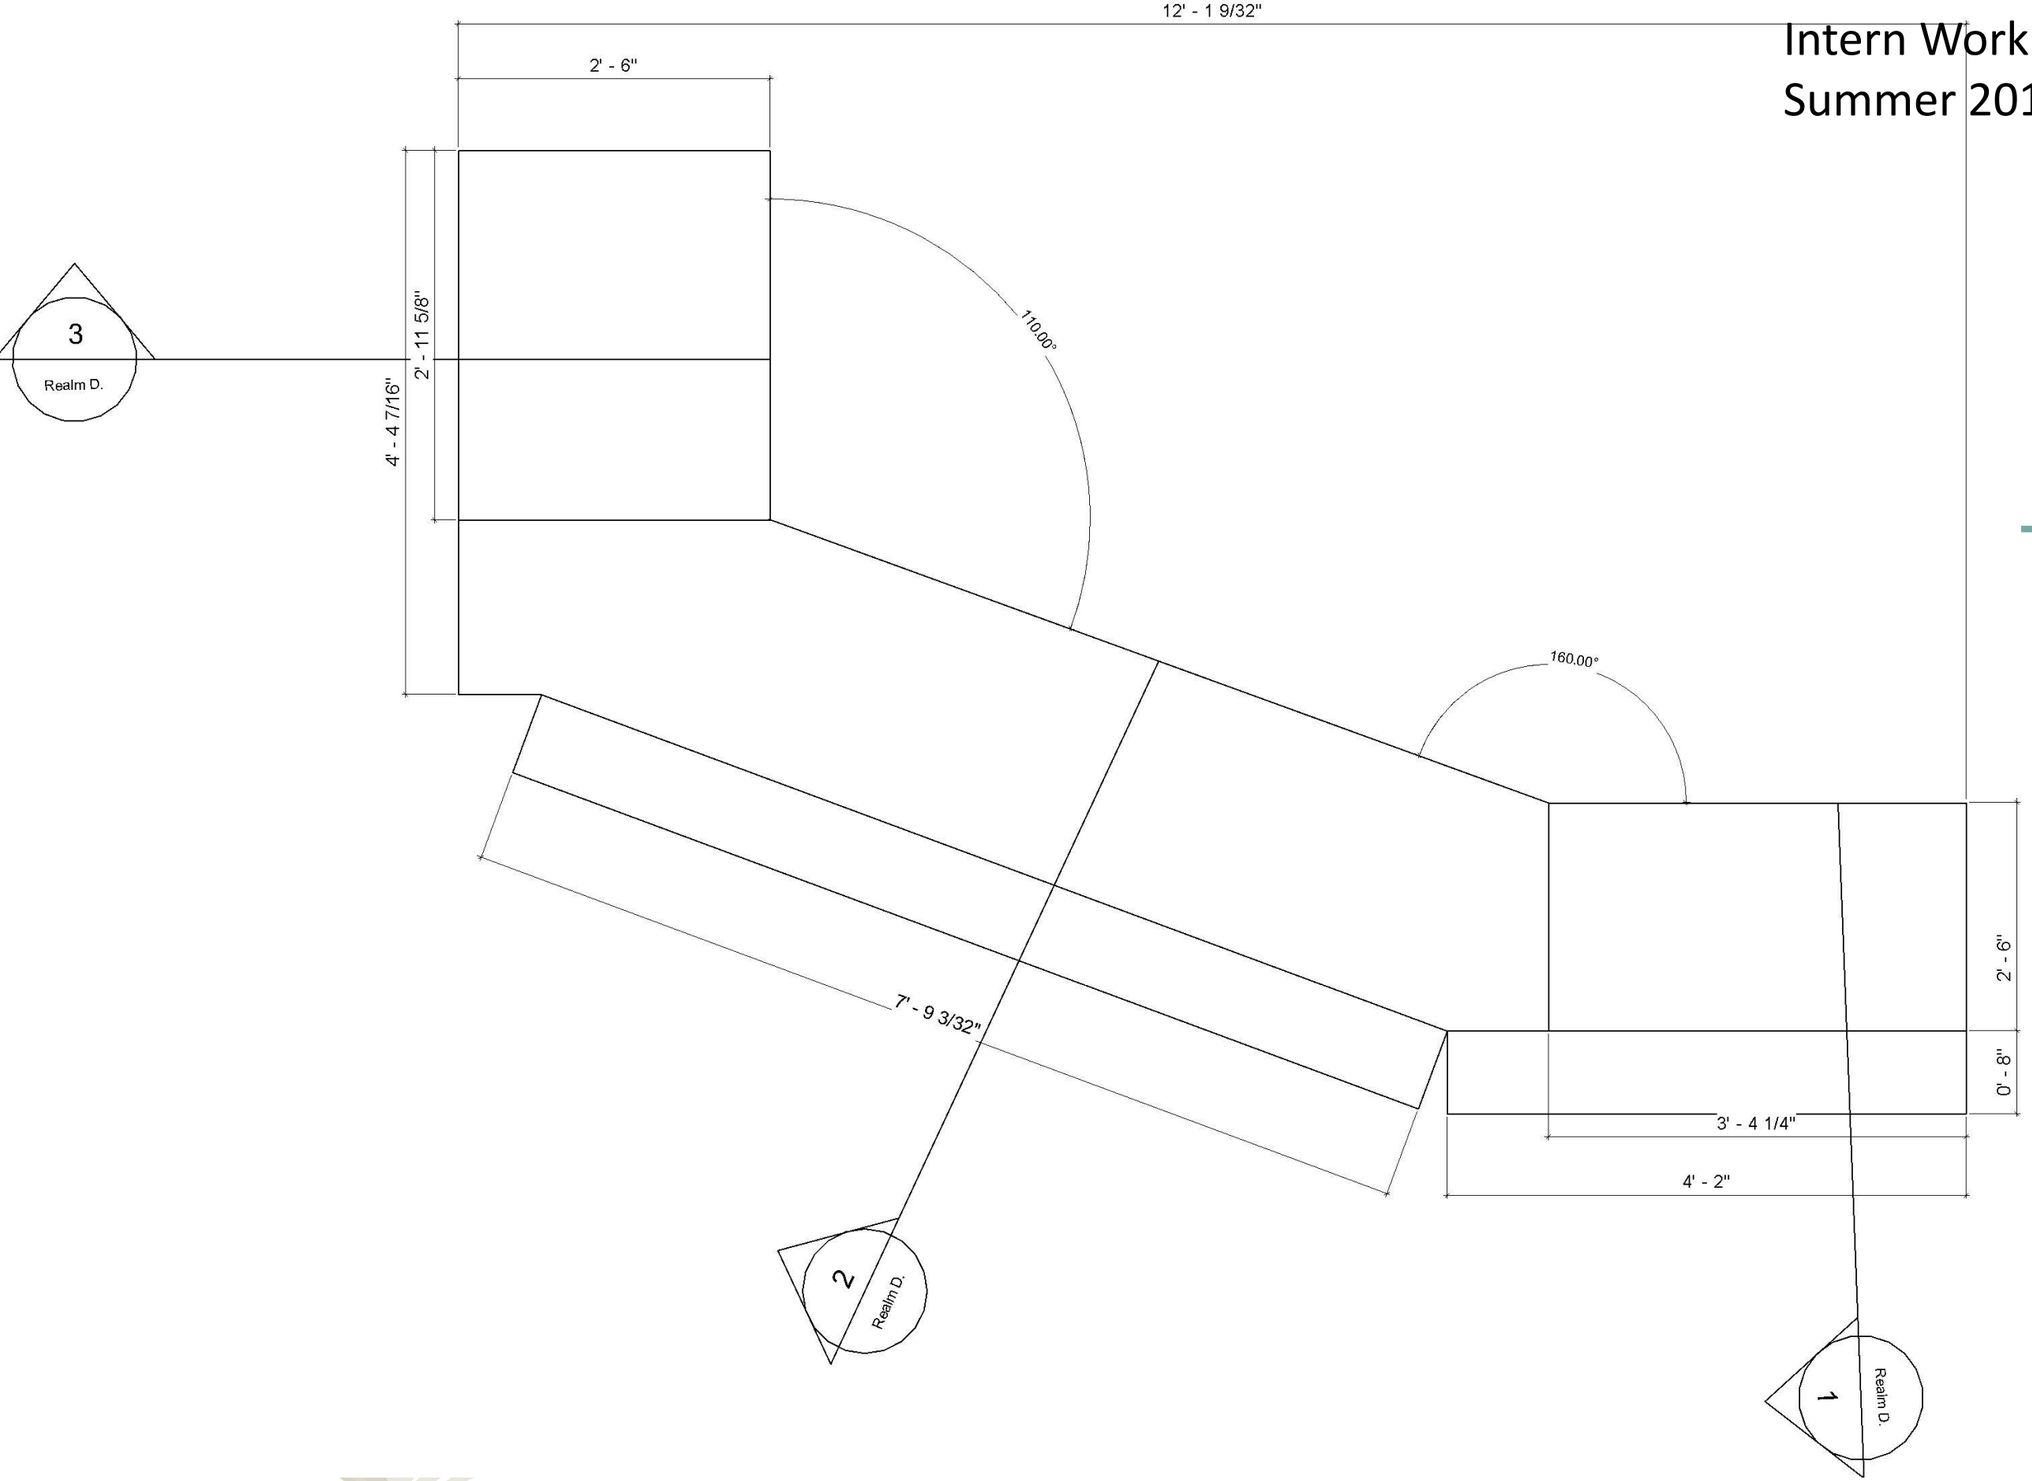

Realm Custom Desk Detail: Plan View

Intern Work from Pedini Atlanta/LBID

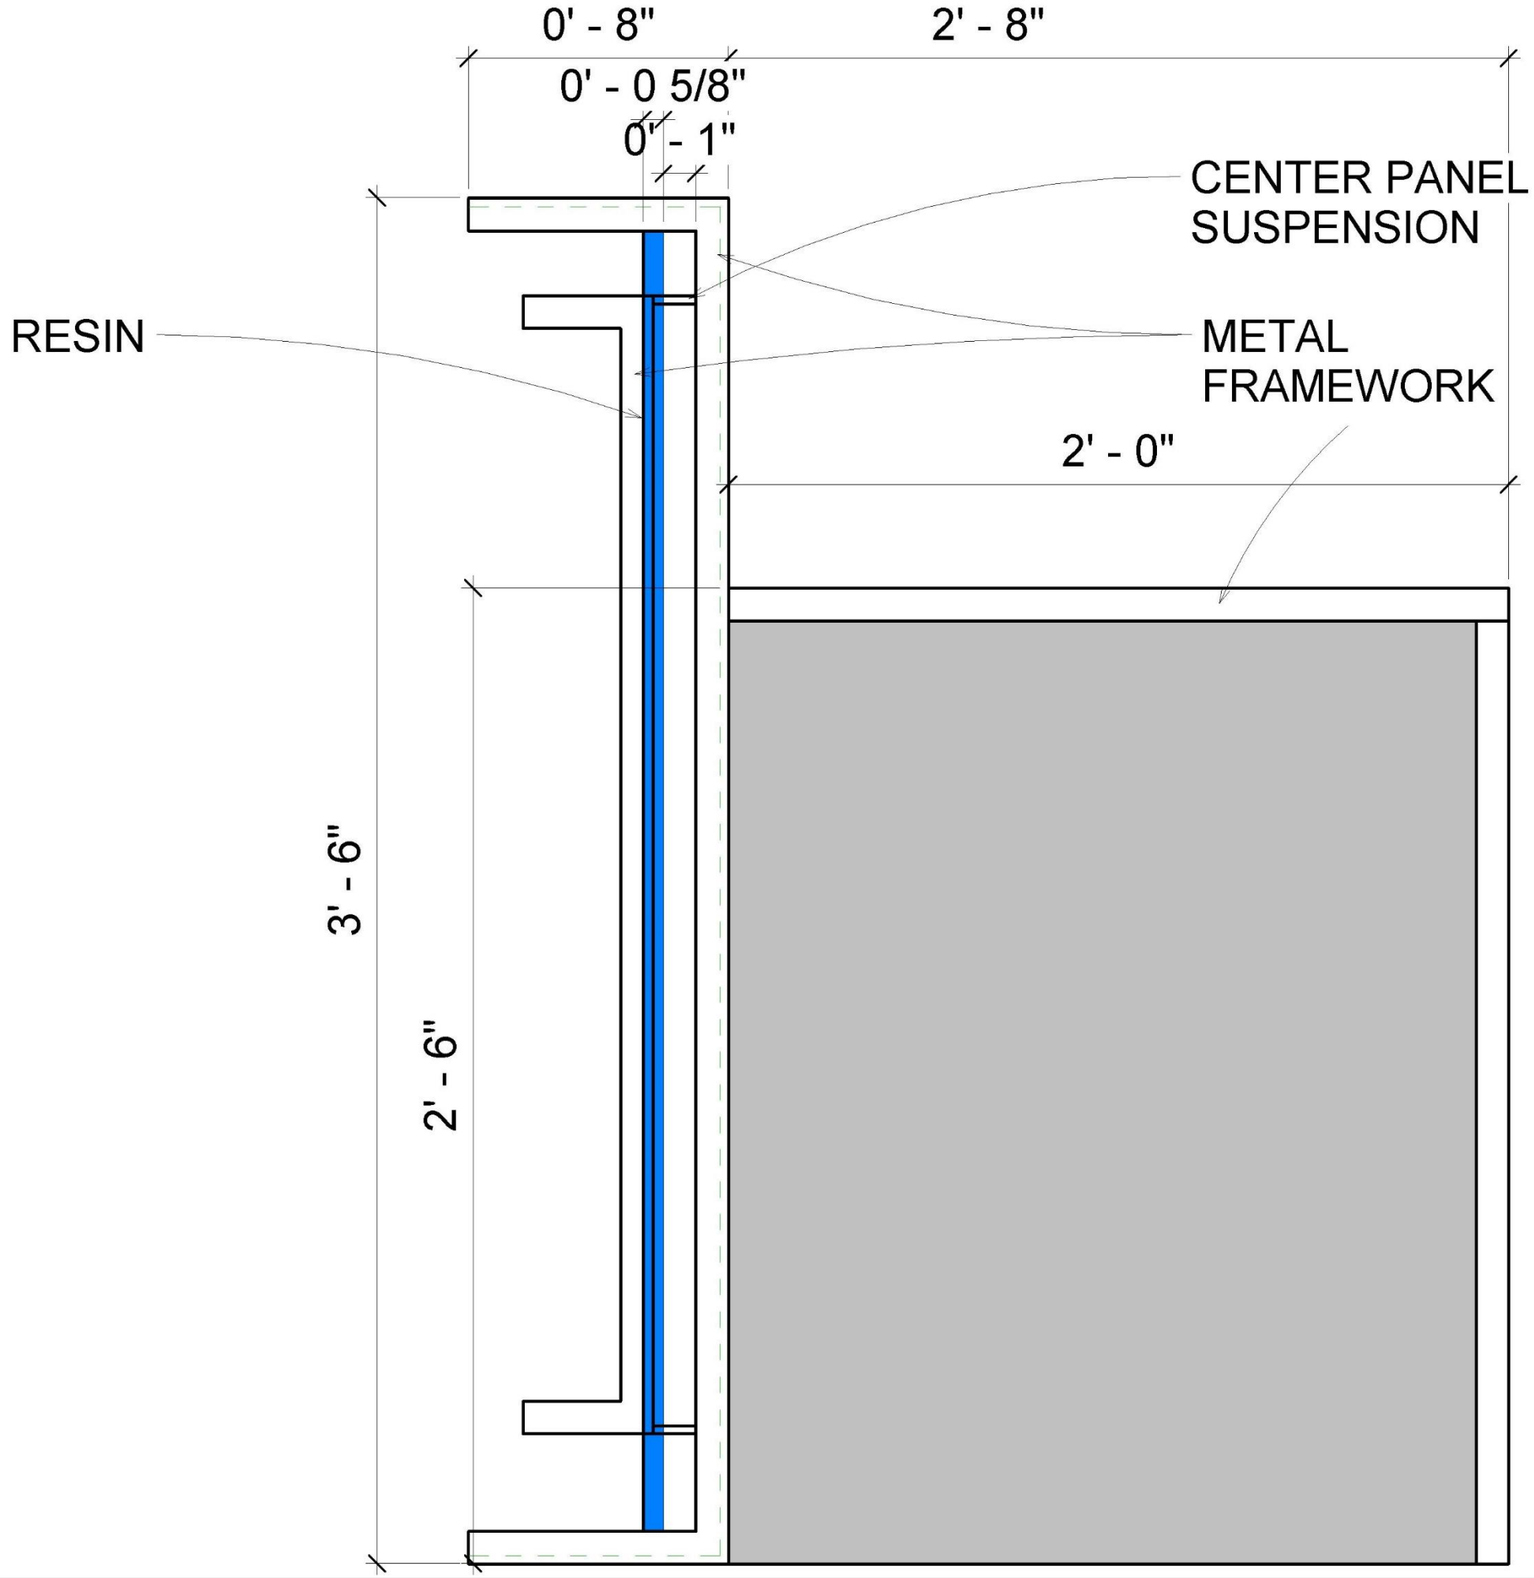

Realm Custom Desk Detail: Section 1

Intern Work from Pedini Atlanta/LBID

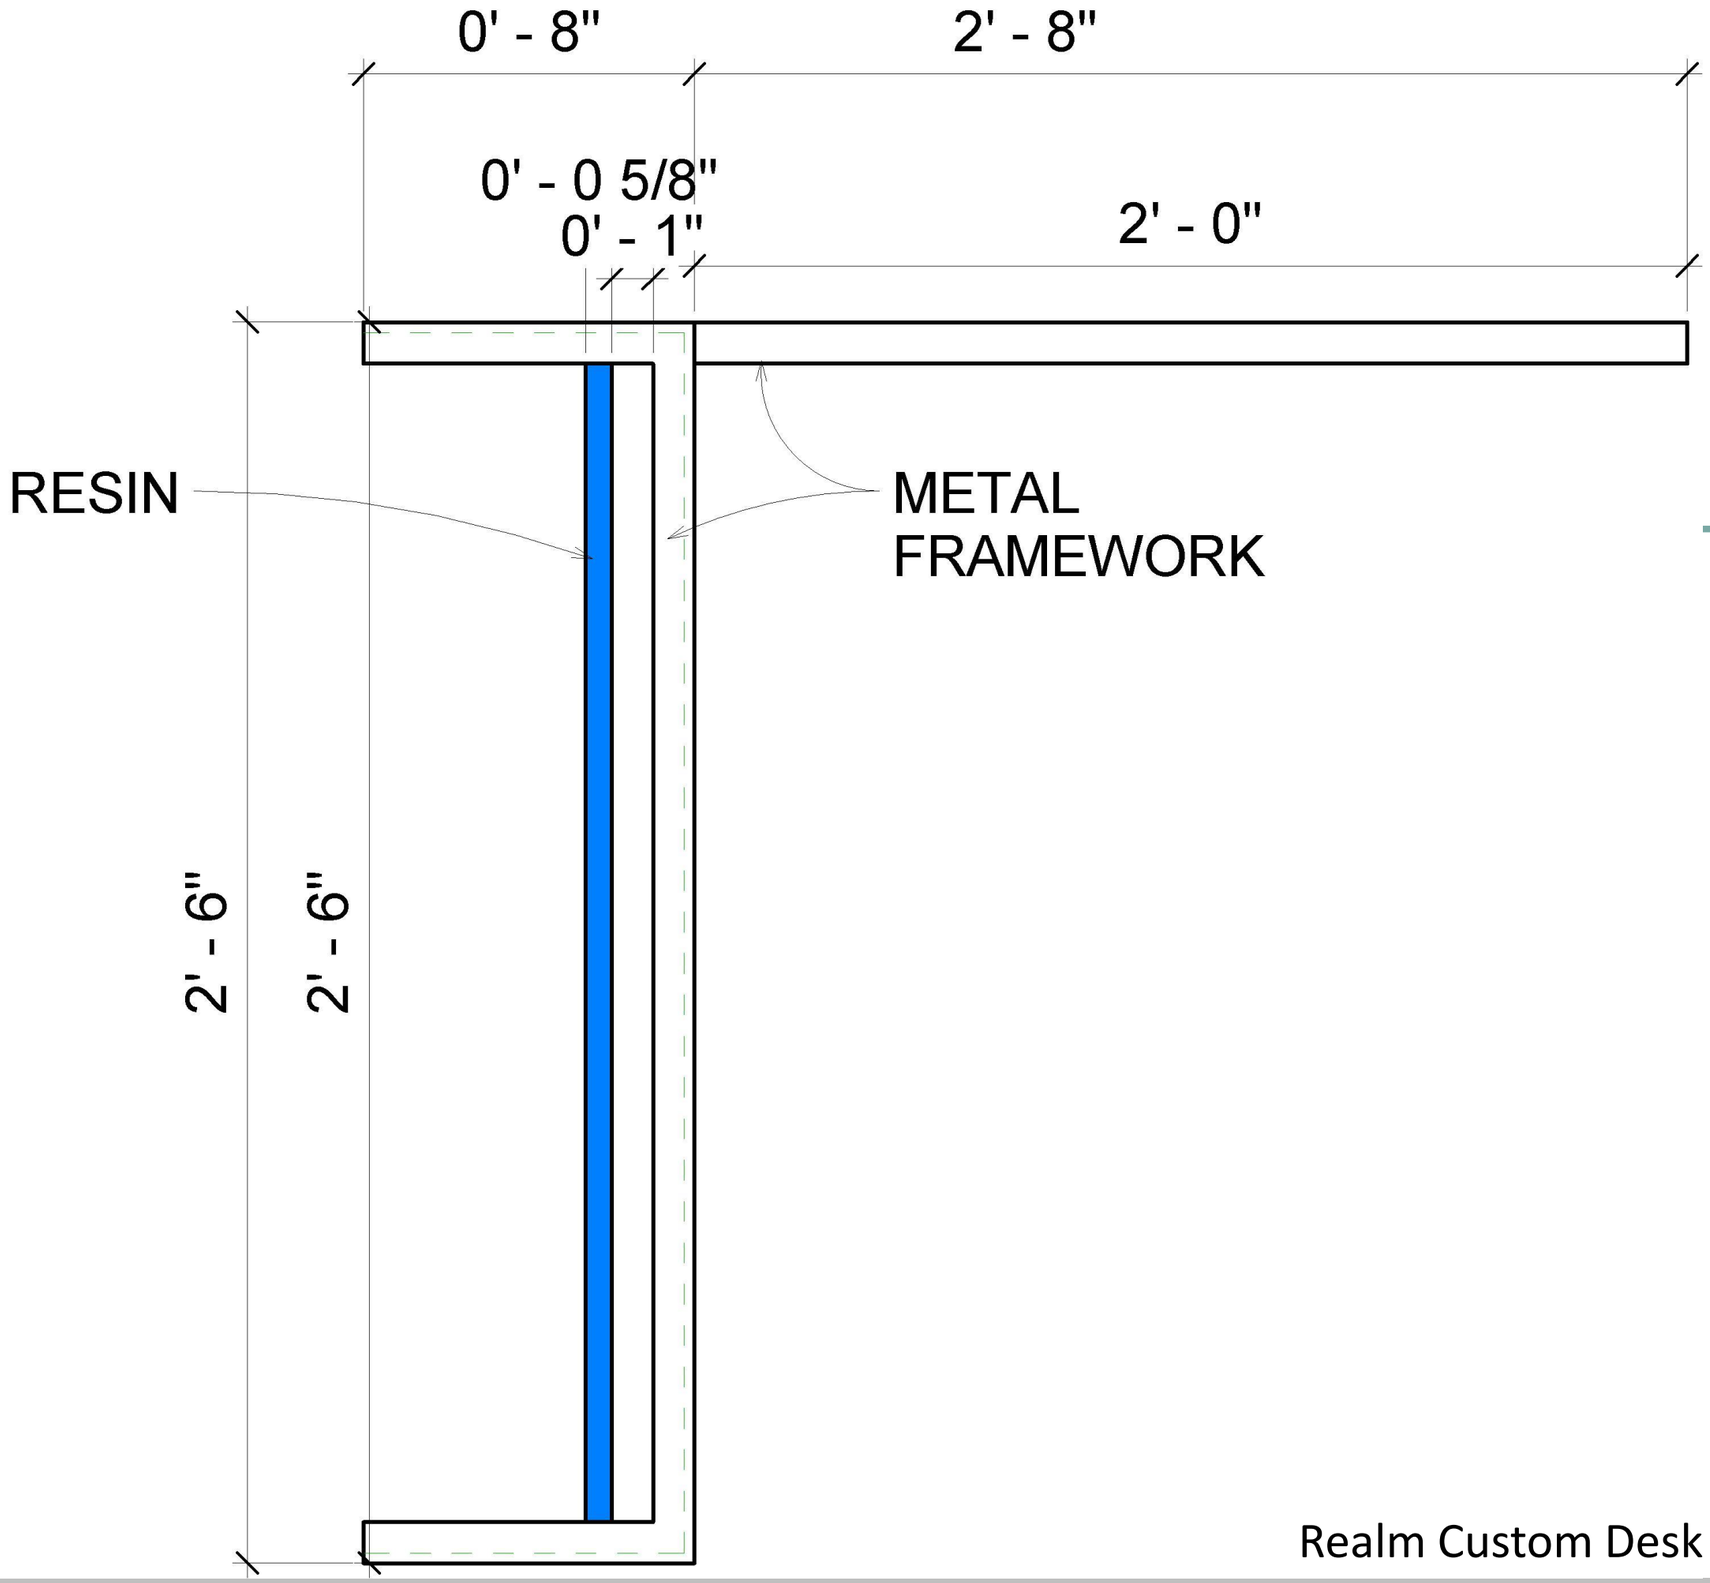

Realm Custom Desk Detail: Section 2

Intern Work from Pedini Atlanta/LBID

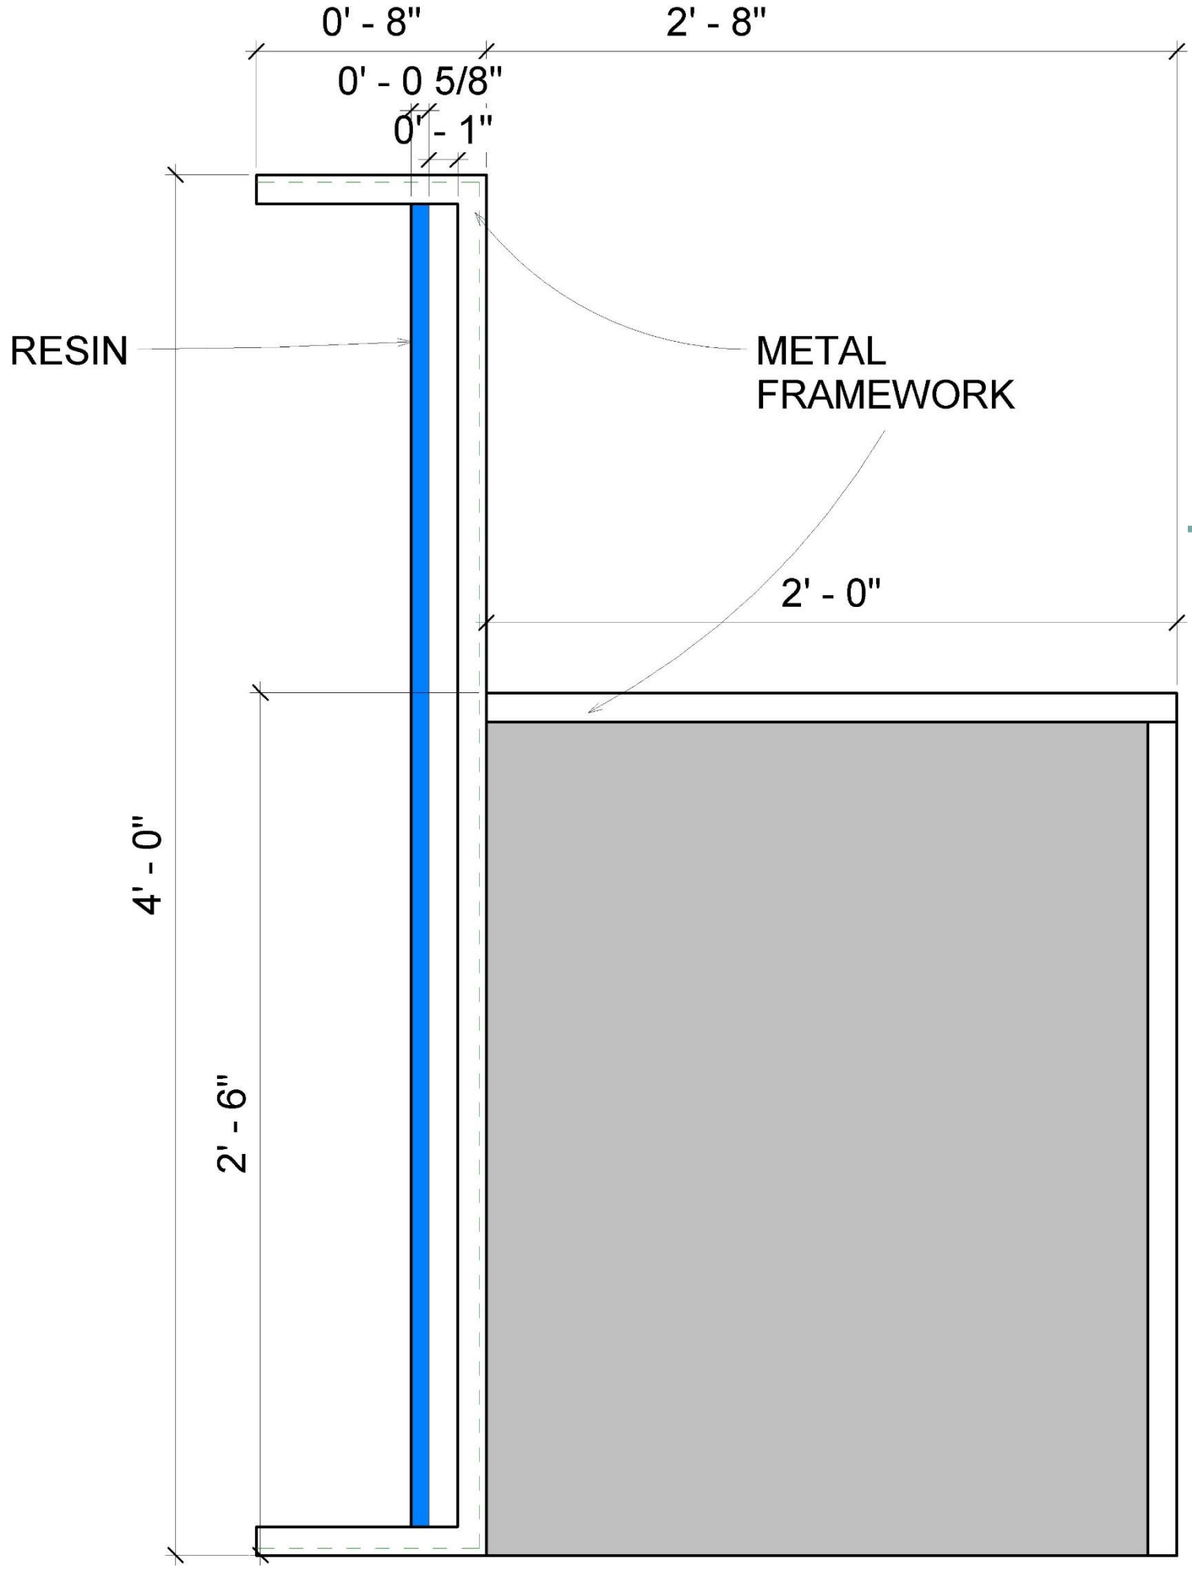

Realm Custom Desk Detail: Section 3

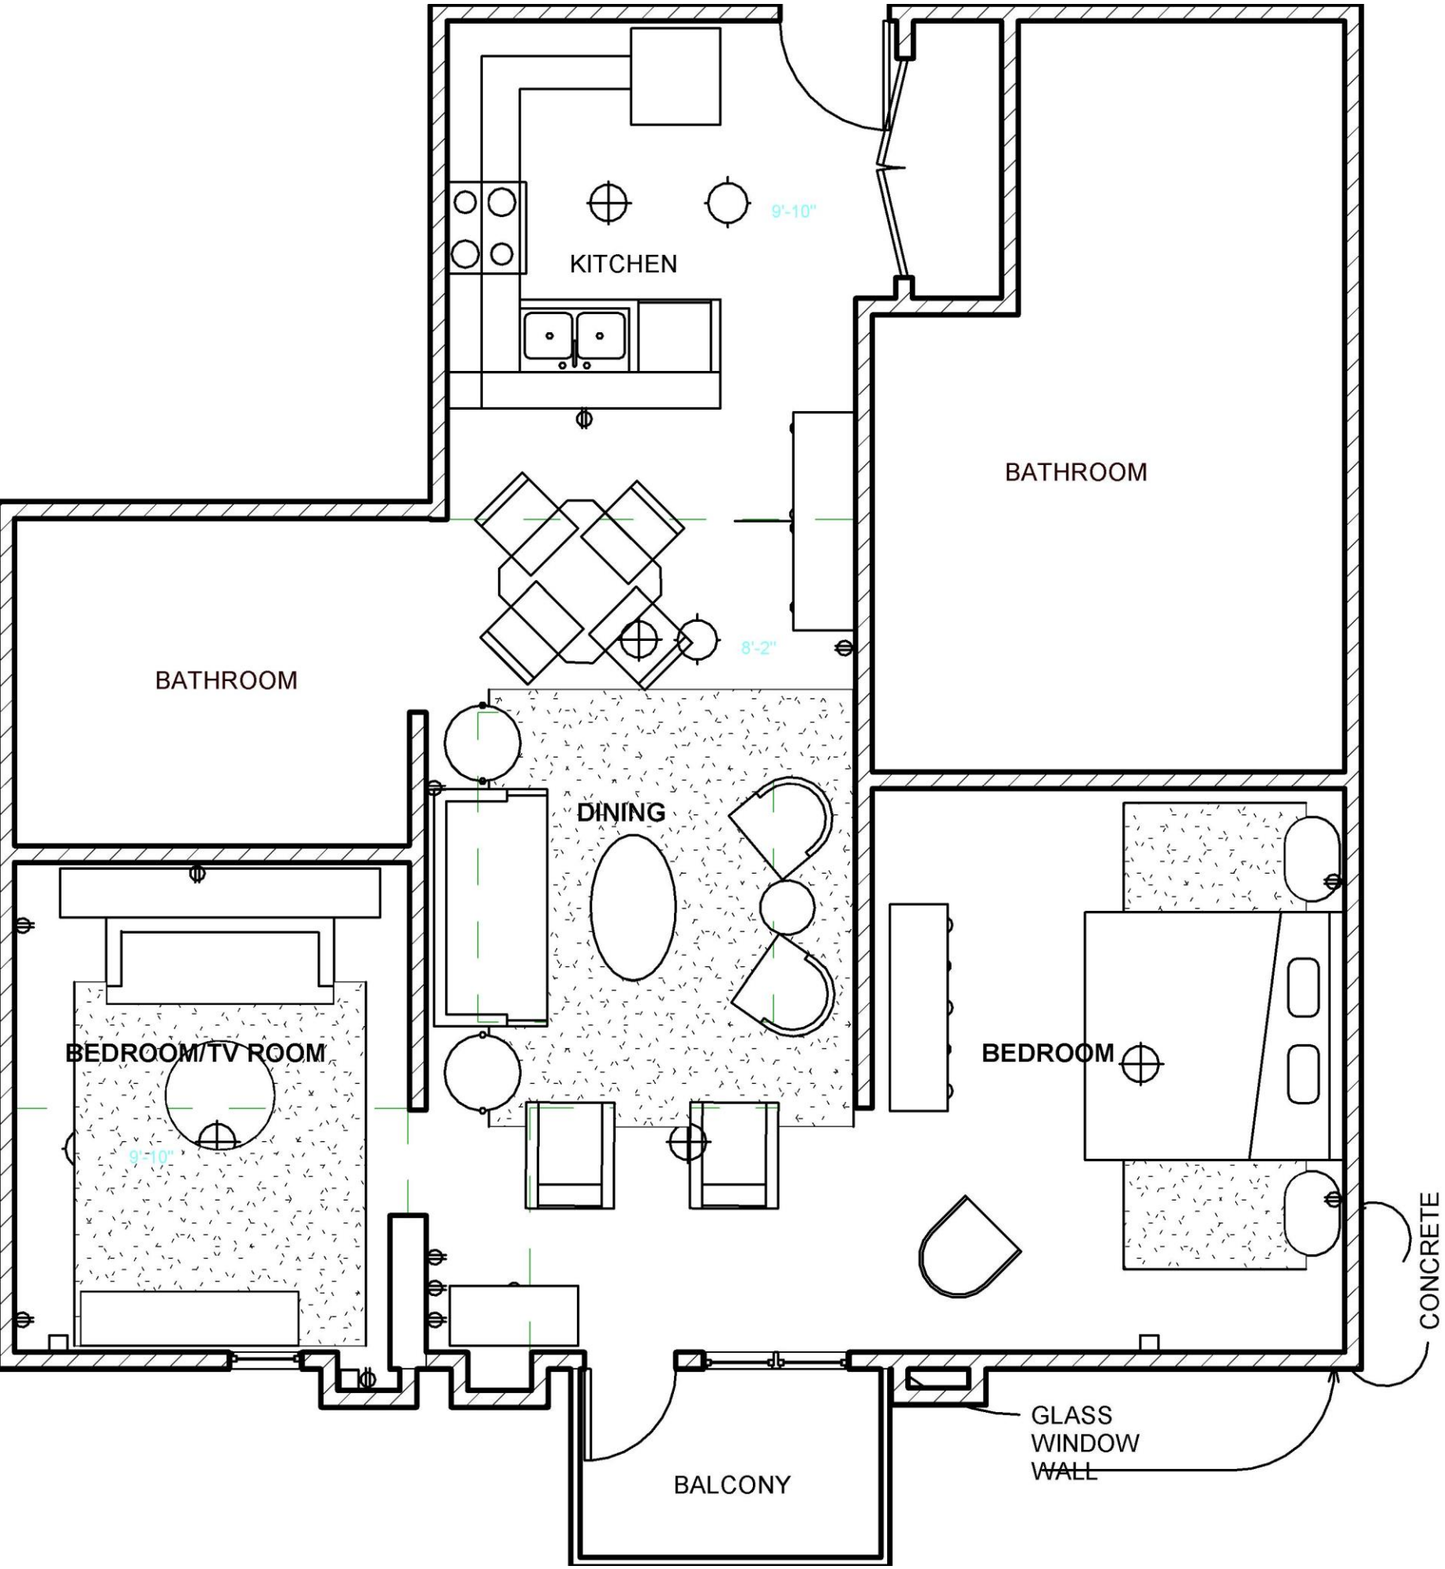

Residence 571: Floor Plan

Intern Work from Pedini Atlanta/LBID

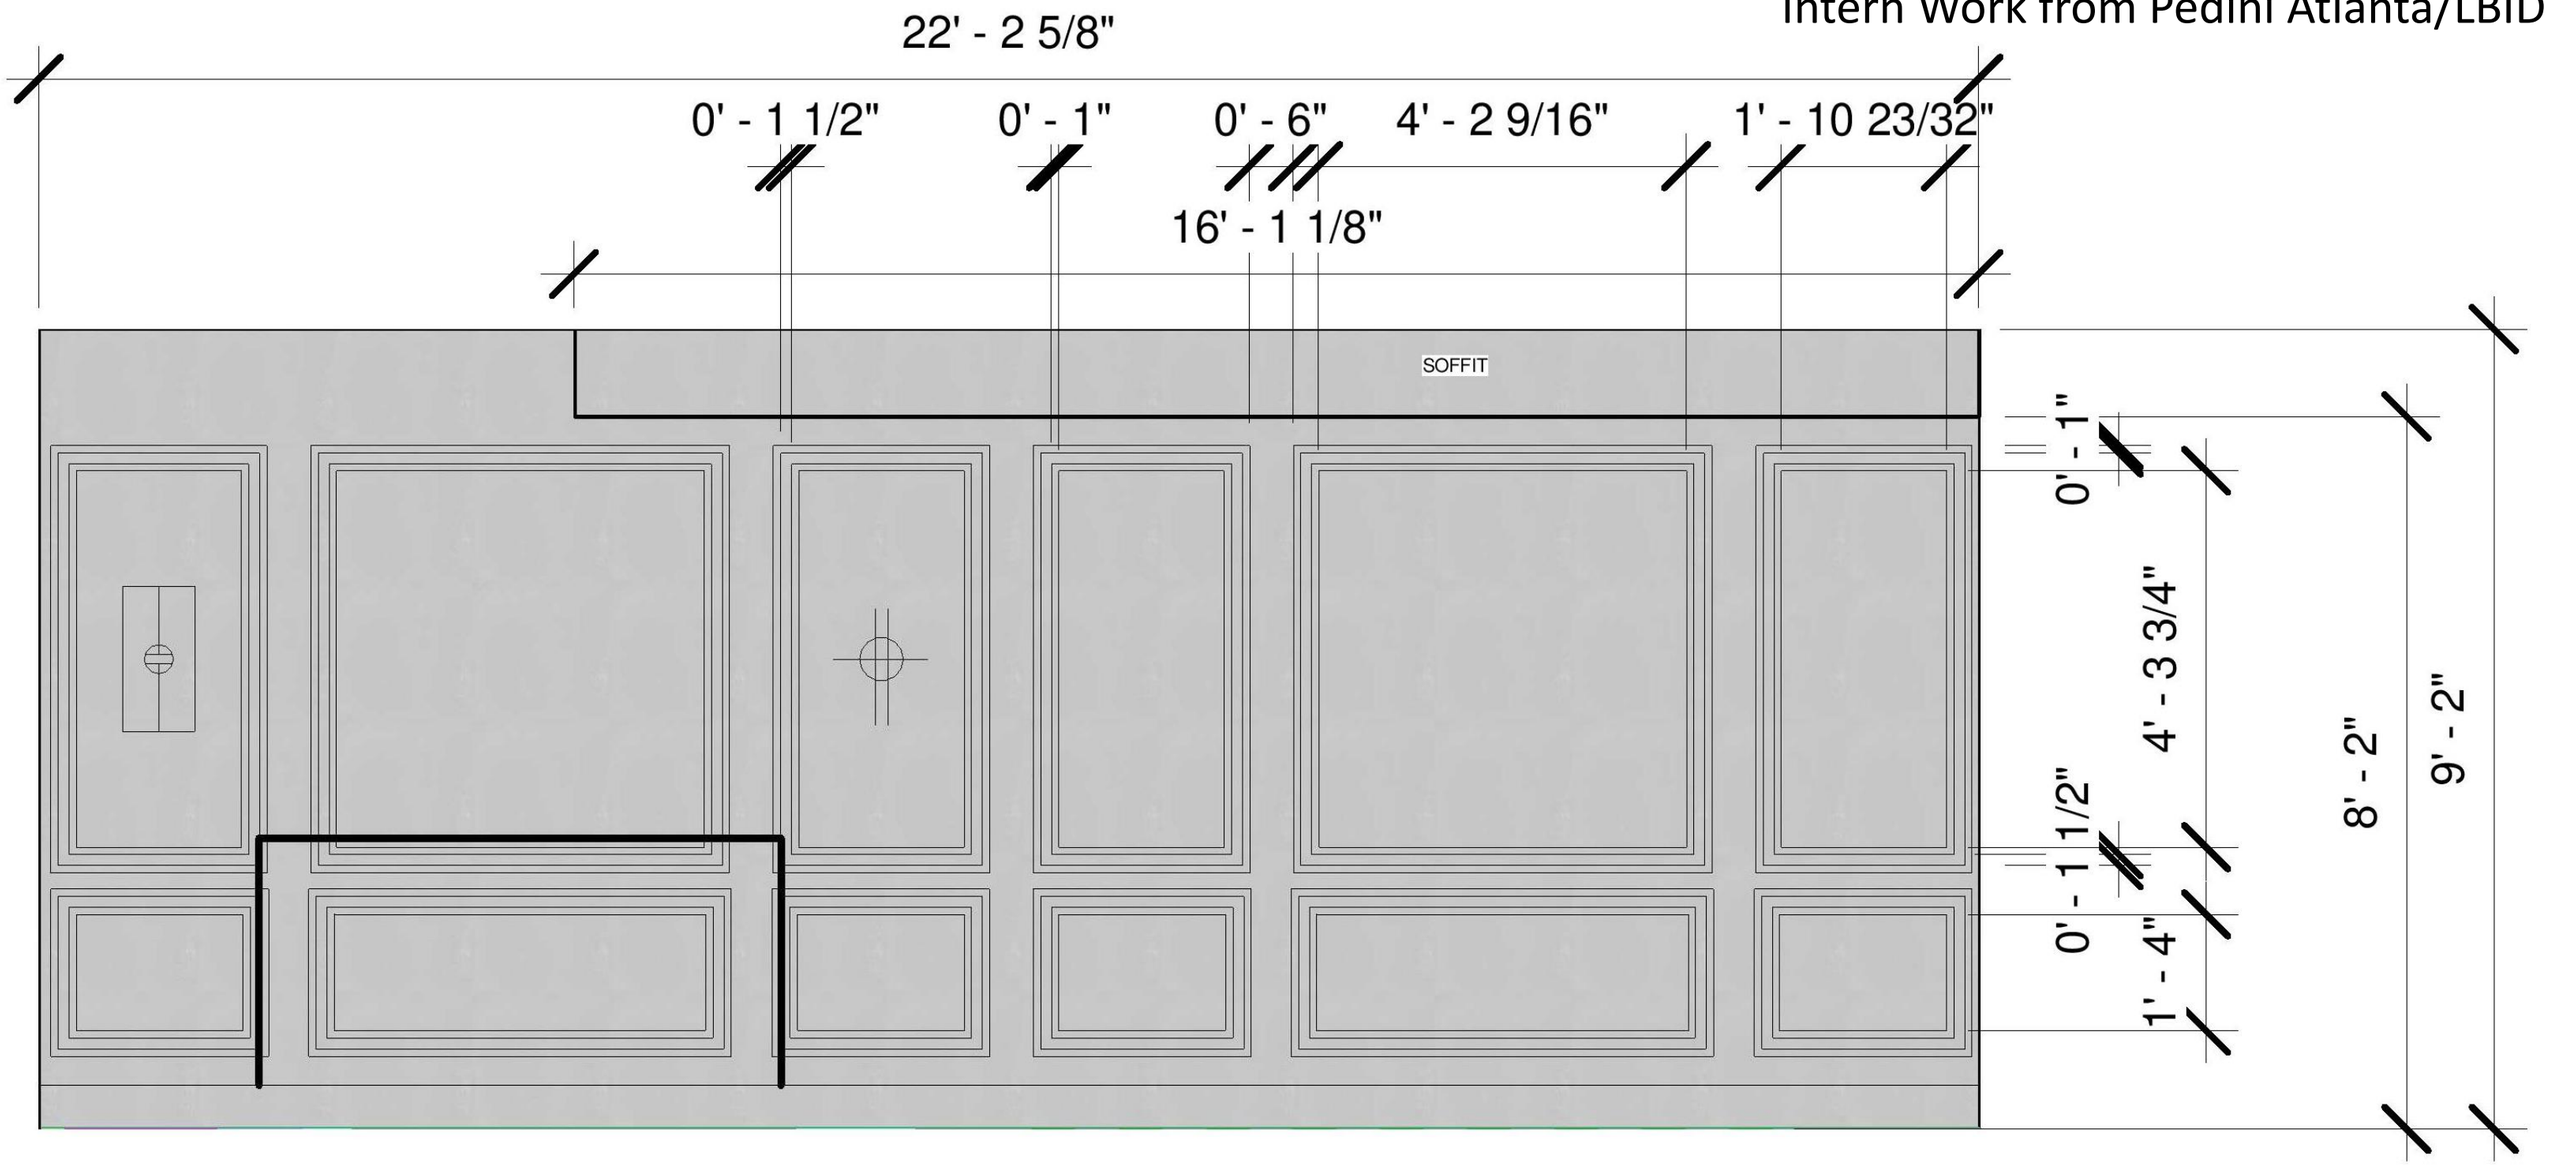

Residence 571: Living Room Elevation

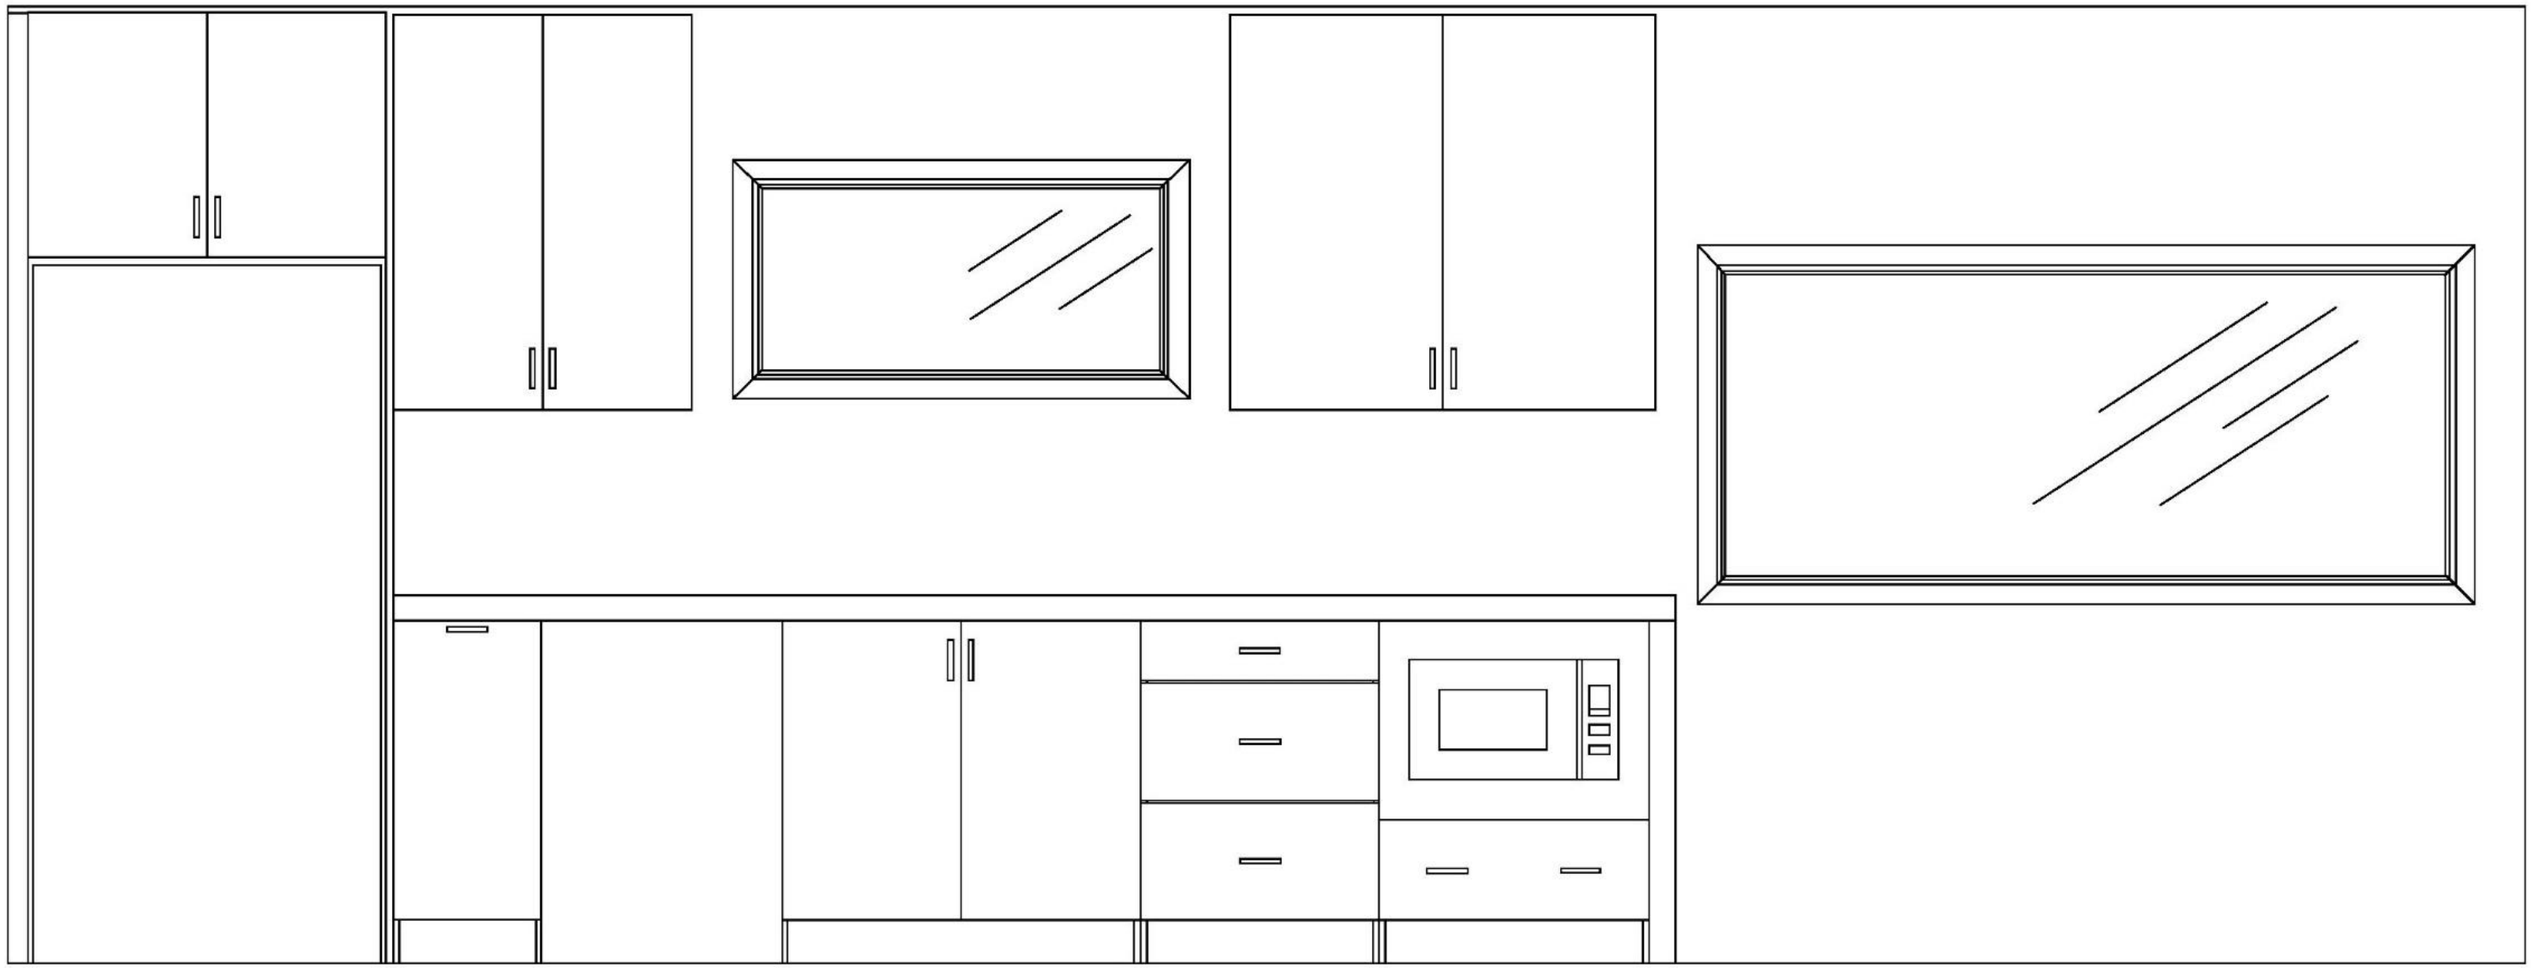

Uri Vaknin Residence: Elevation